


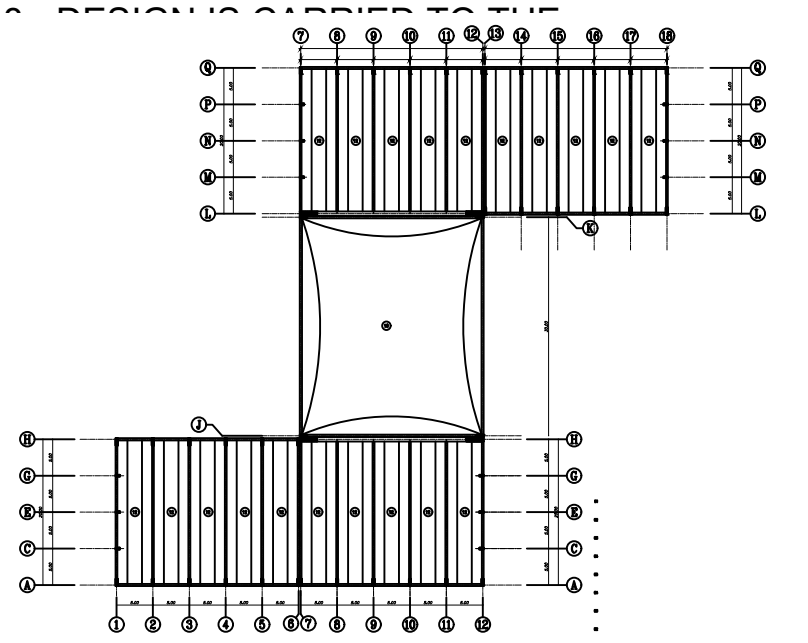

Faculty of Engineering
Cairo University
Civil Department

NOTES :

- 1- ALL DIMENSIONS AND AXES SHOULD BE READ IN CONJUNCTION WITH ARCHITECTURAL DRAWINGS BEFORE CONSTRUCTION.
- 2 - ALL DIMENSION AND LEVELS ARE IN M UNLESS OTHERWISE NOTED ON PLAN.
- 3 - THE CUBIC STRENGTH OF R. CONCRETE USED IN ALL R.C. WORKS AFTER 28 DAYS SHOULD NOT BE LESS THAN 250 Kg/cm².
- 4 - THE CEMENT USED FOR BOTH PLAIN AND REINFORCED CONCRETE UNDER GROUND LEVEL IS SULPHATE RESISTENCE PORTLAND CEMENT.
- 5 - STEEL USED IN RFT. IN R.C. WORK IS HIGH TENSILE STEEL "36/54" FOR DIAMETERS 10 mm AND MILD STEEL "24/35" FOR 8mm.
- 6 - THE REINFORCEMENT OF COULMNS WILL BE TAKEN FROM COULMNS DETAILS.
- 7 - CONCRETE COVER SHOULD NOT LESS THAN 2.5 cm FOR COULMNS.



PROJECT NAME :


HALL UNIT

By :


Anas Akram Saeed




DRAWING TITLE :

SECOND FLOOR PLANE

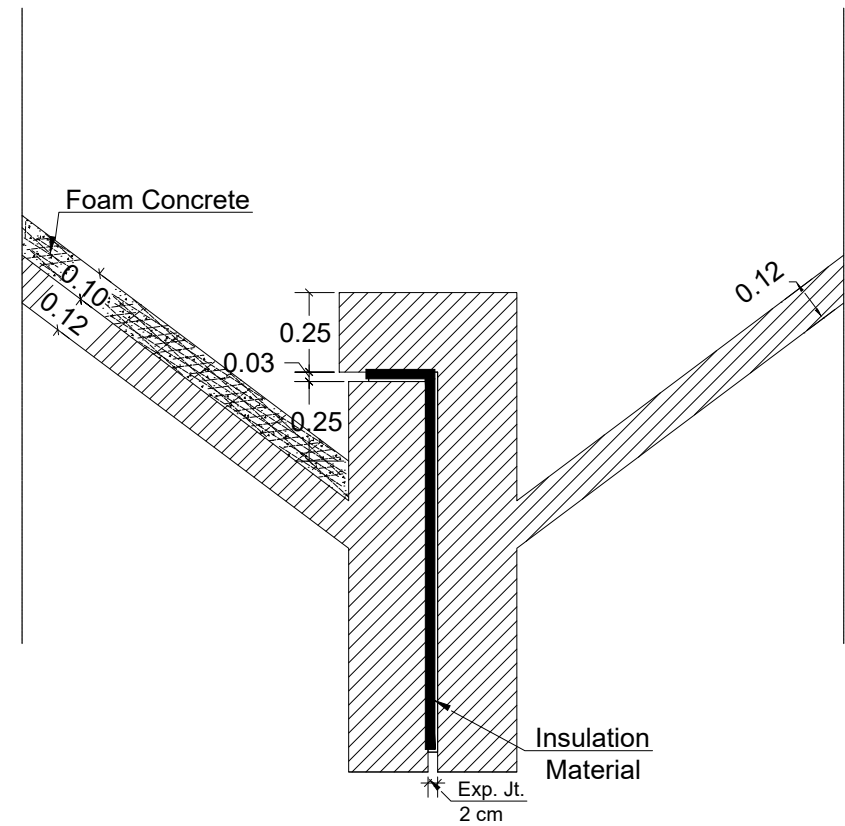

Expansion Joint

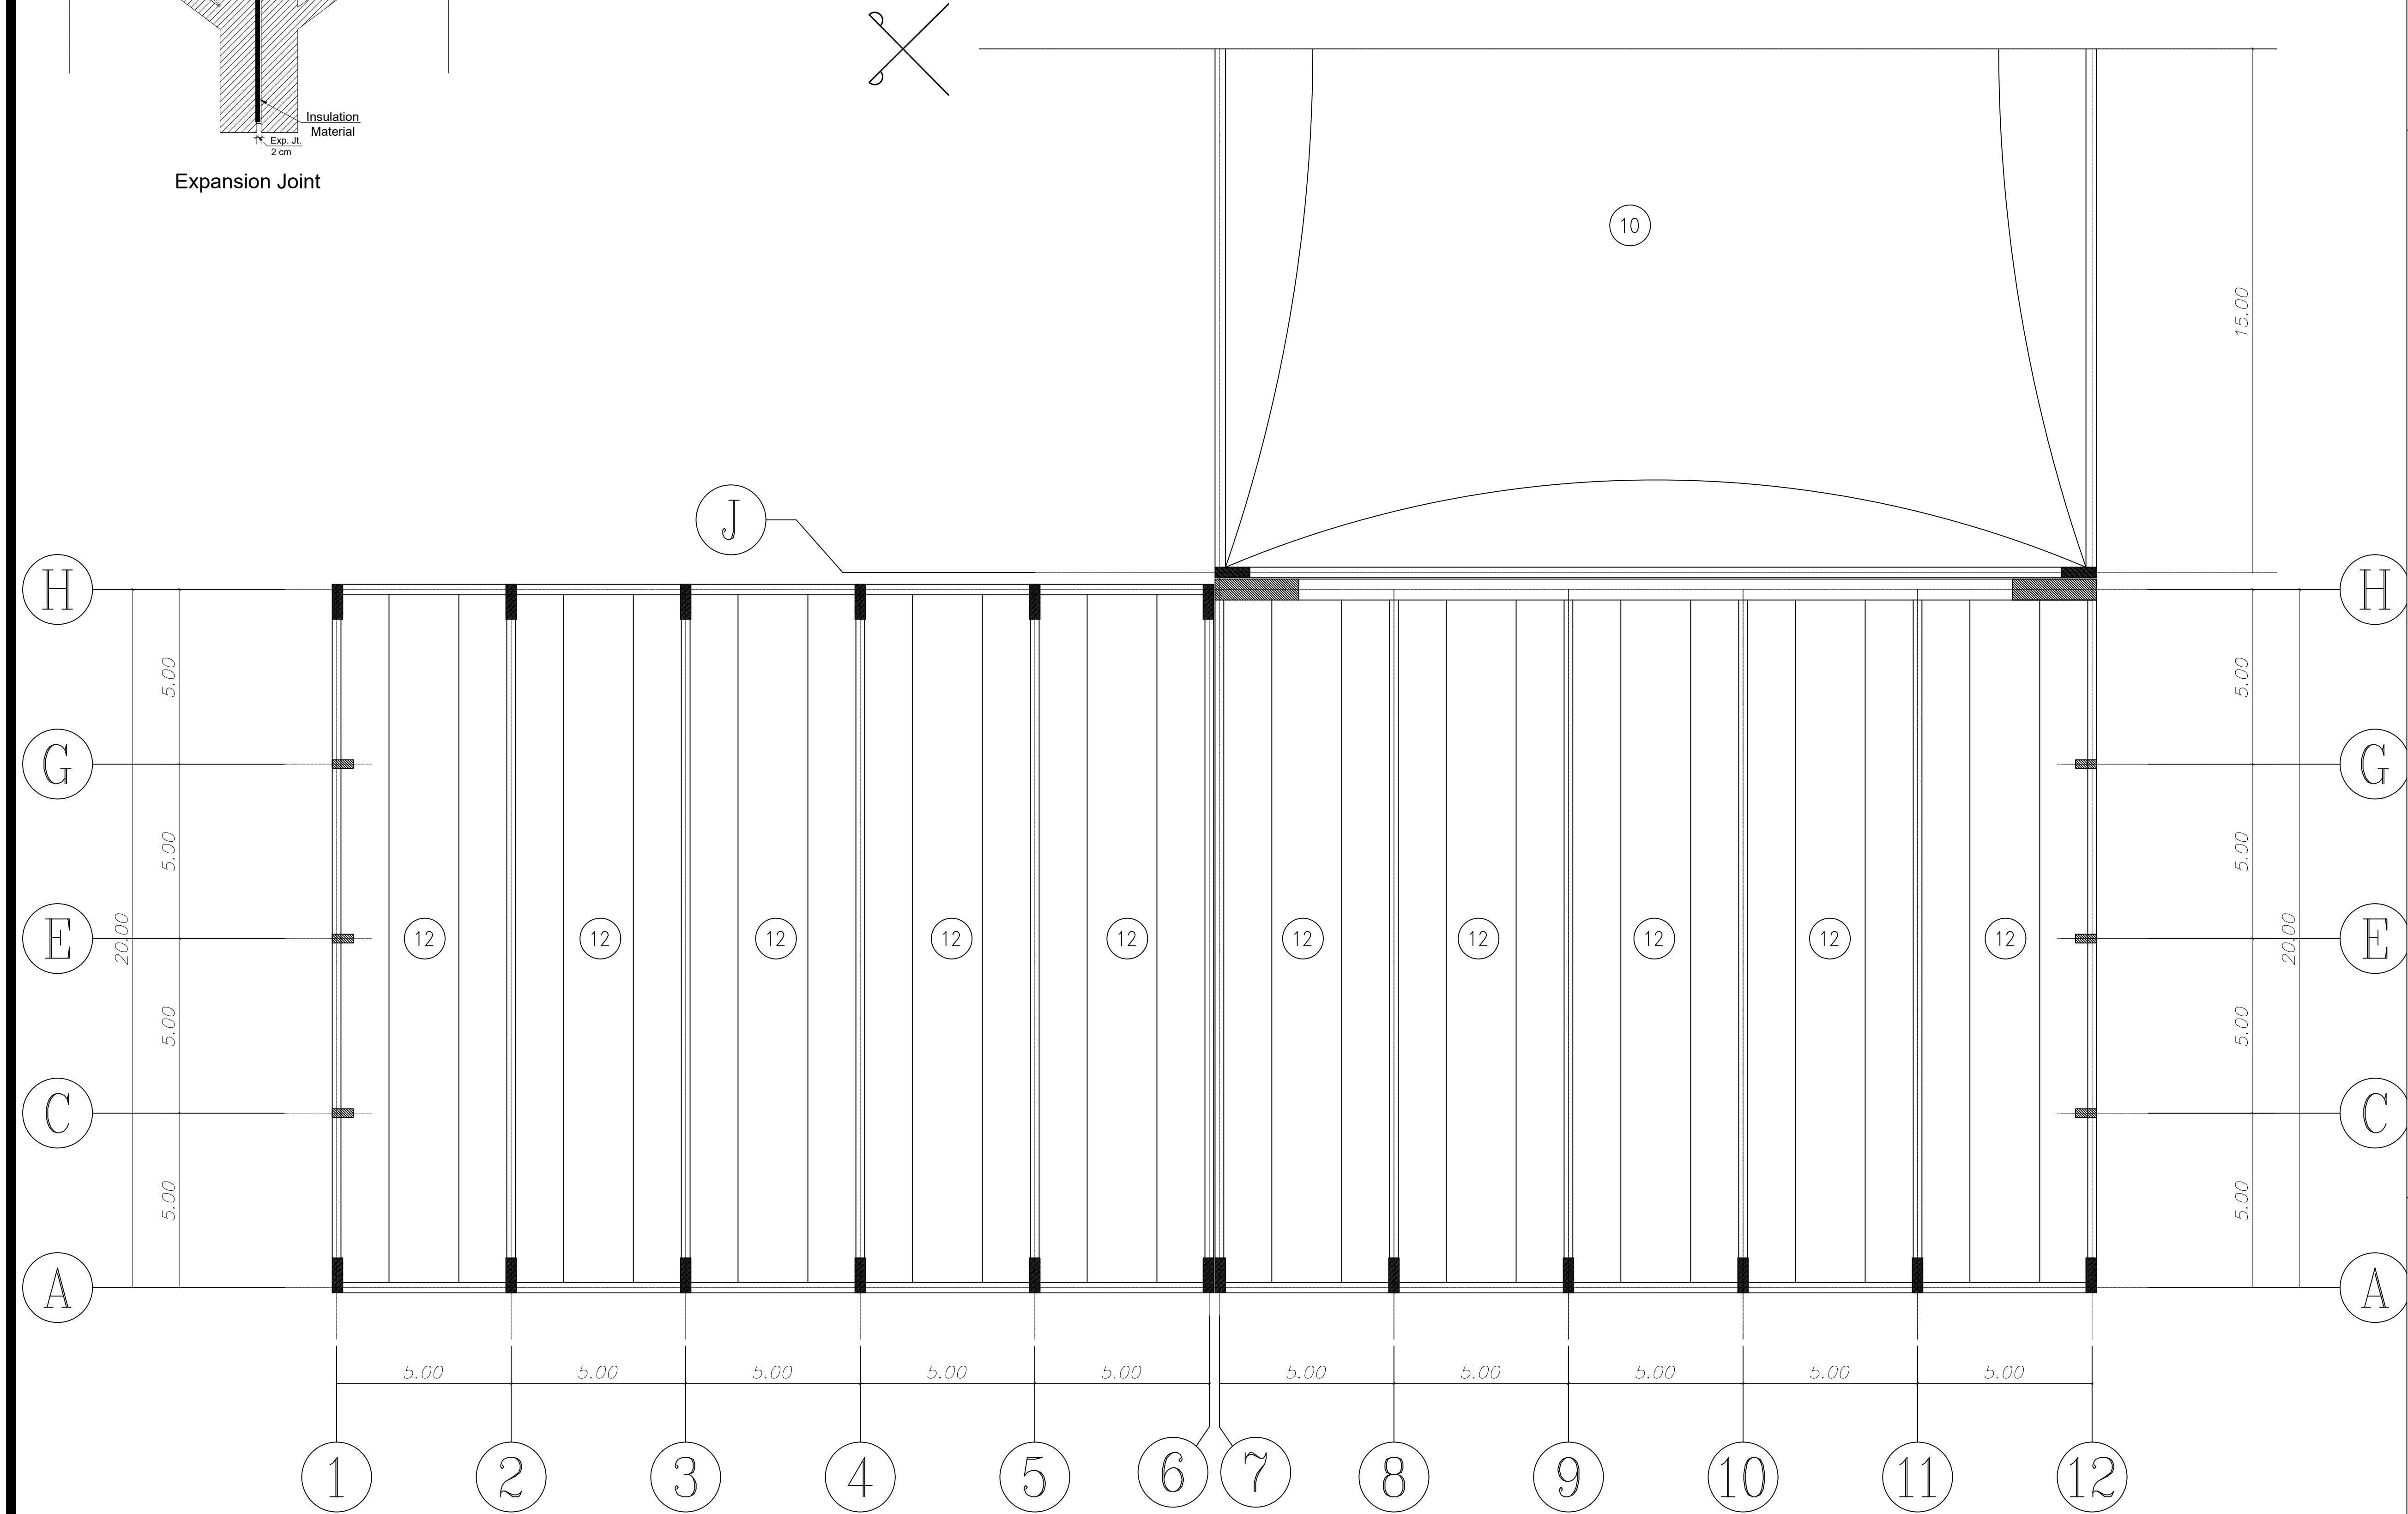


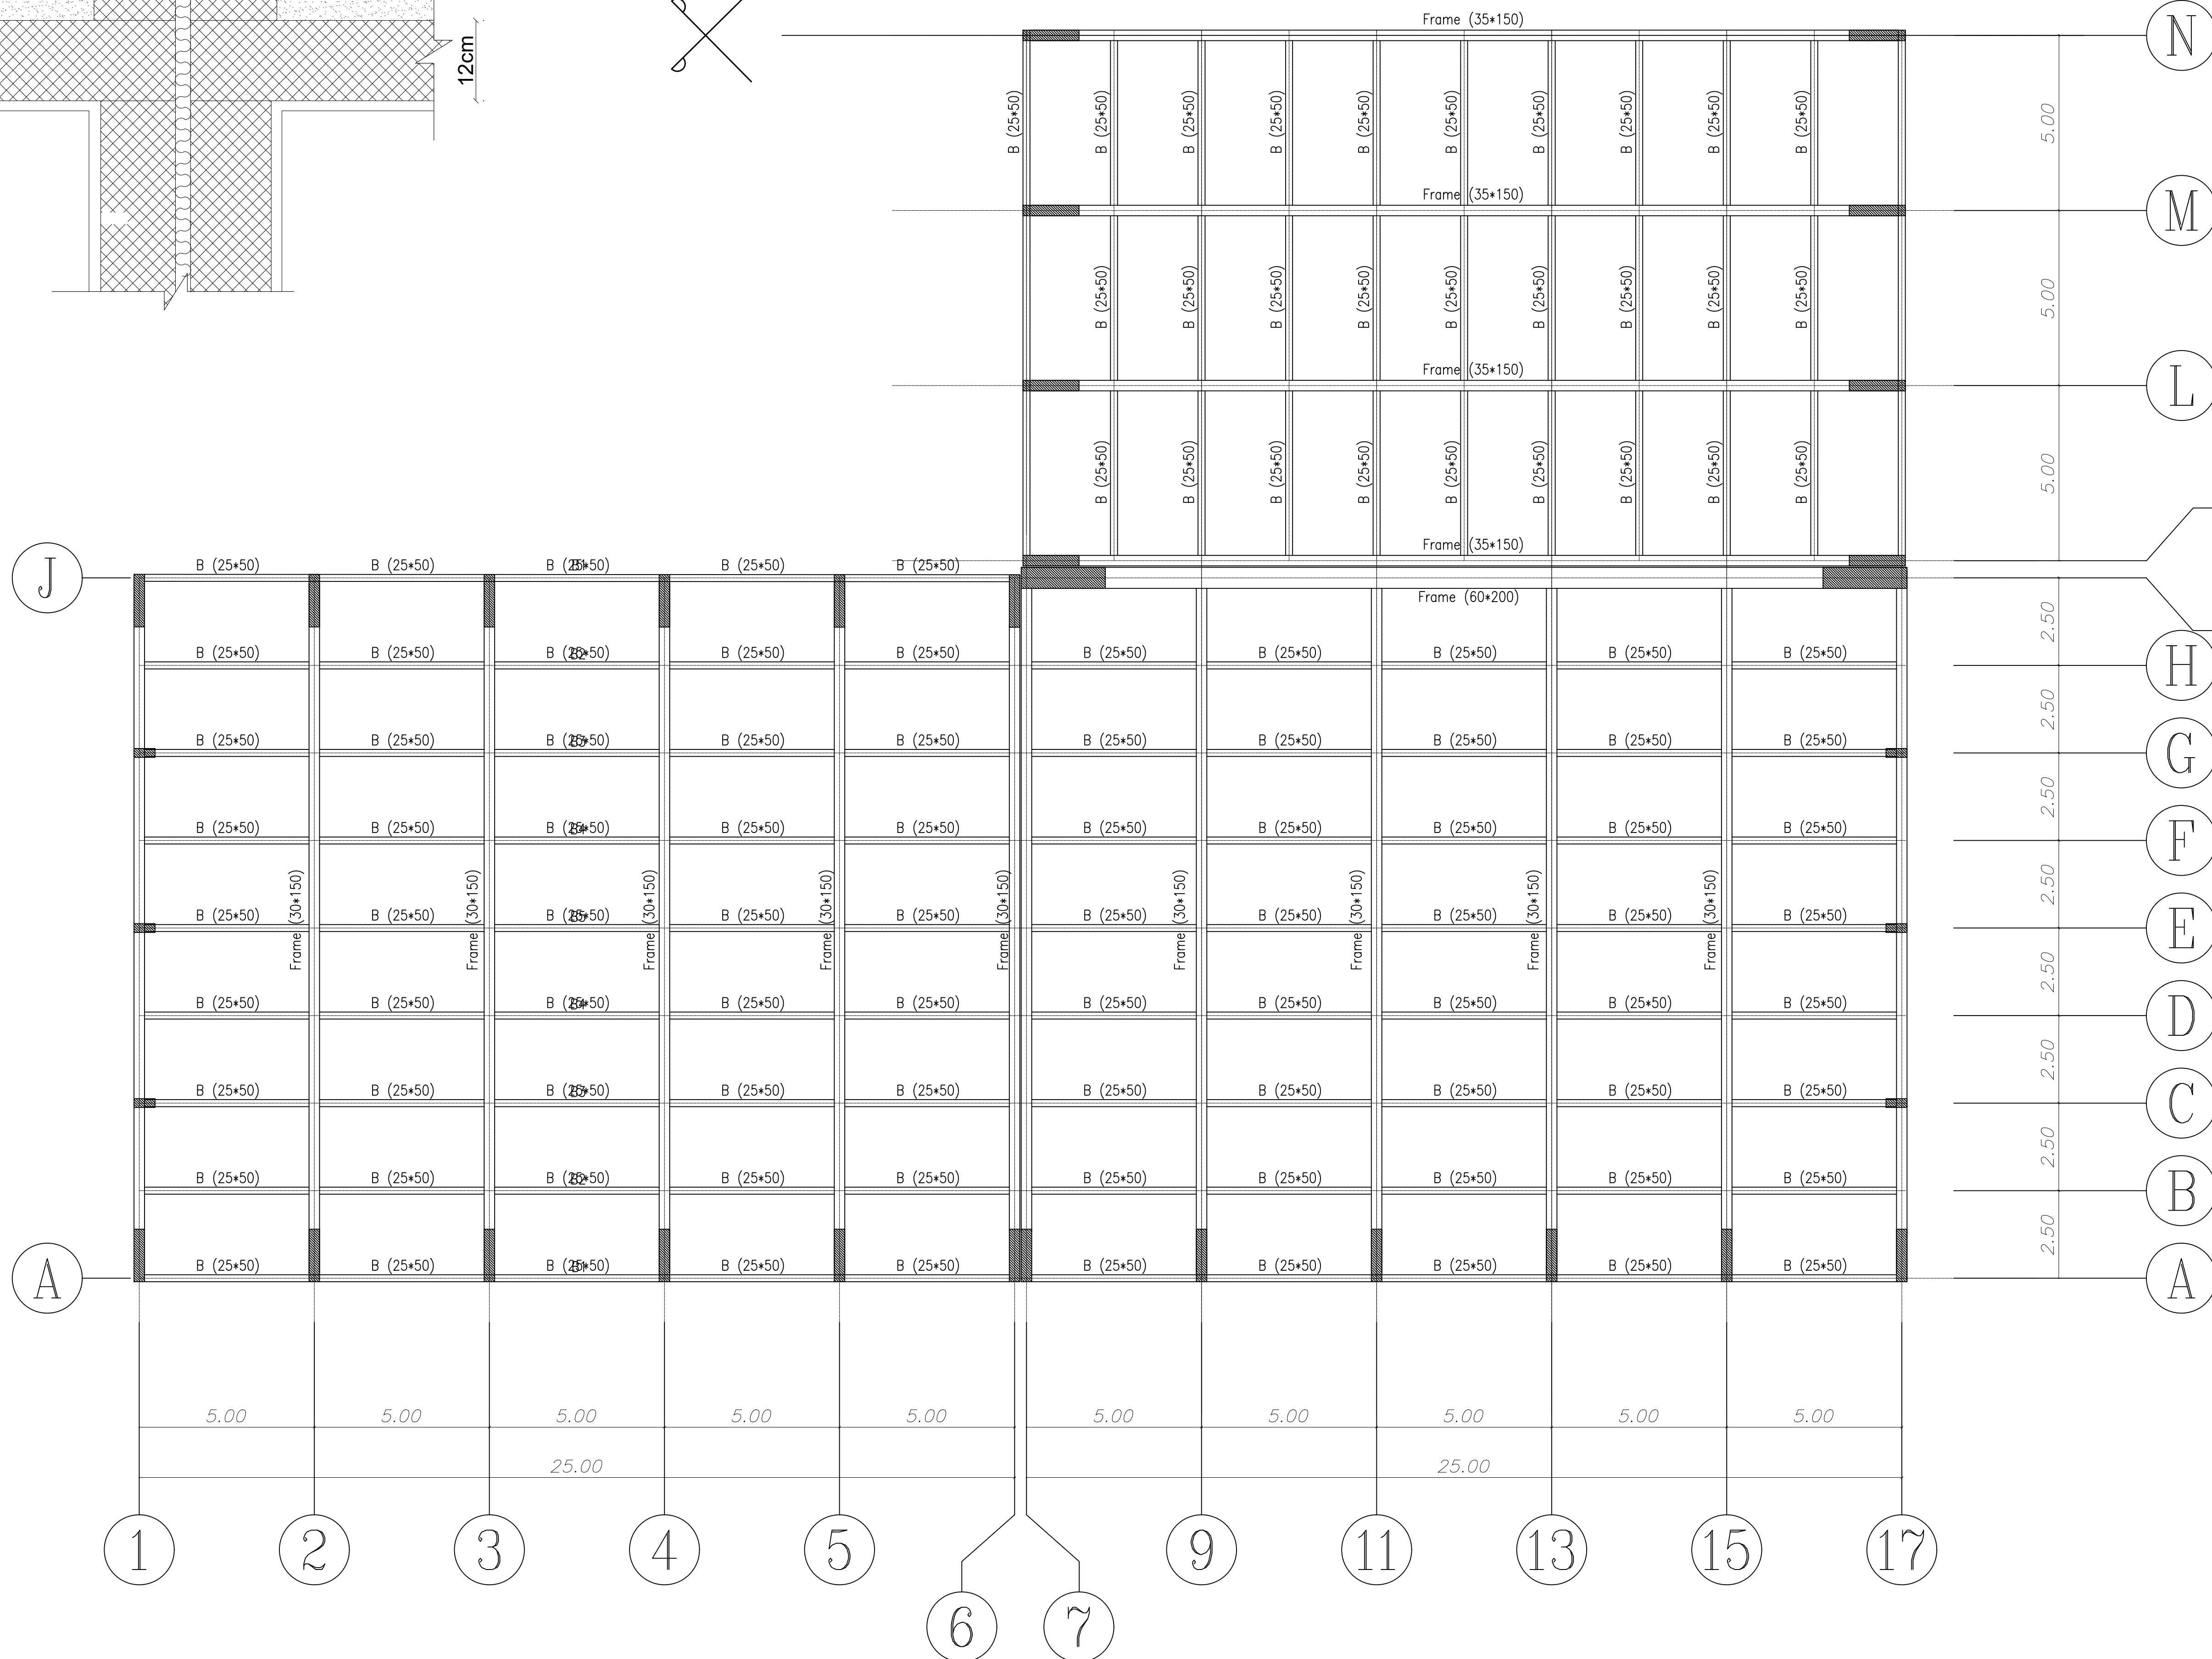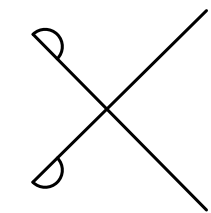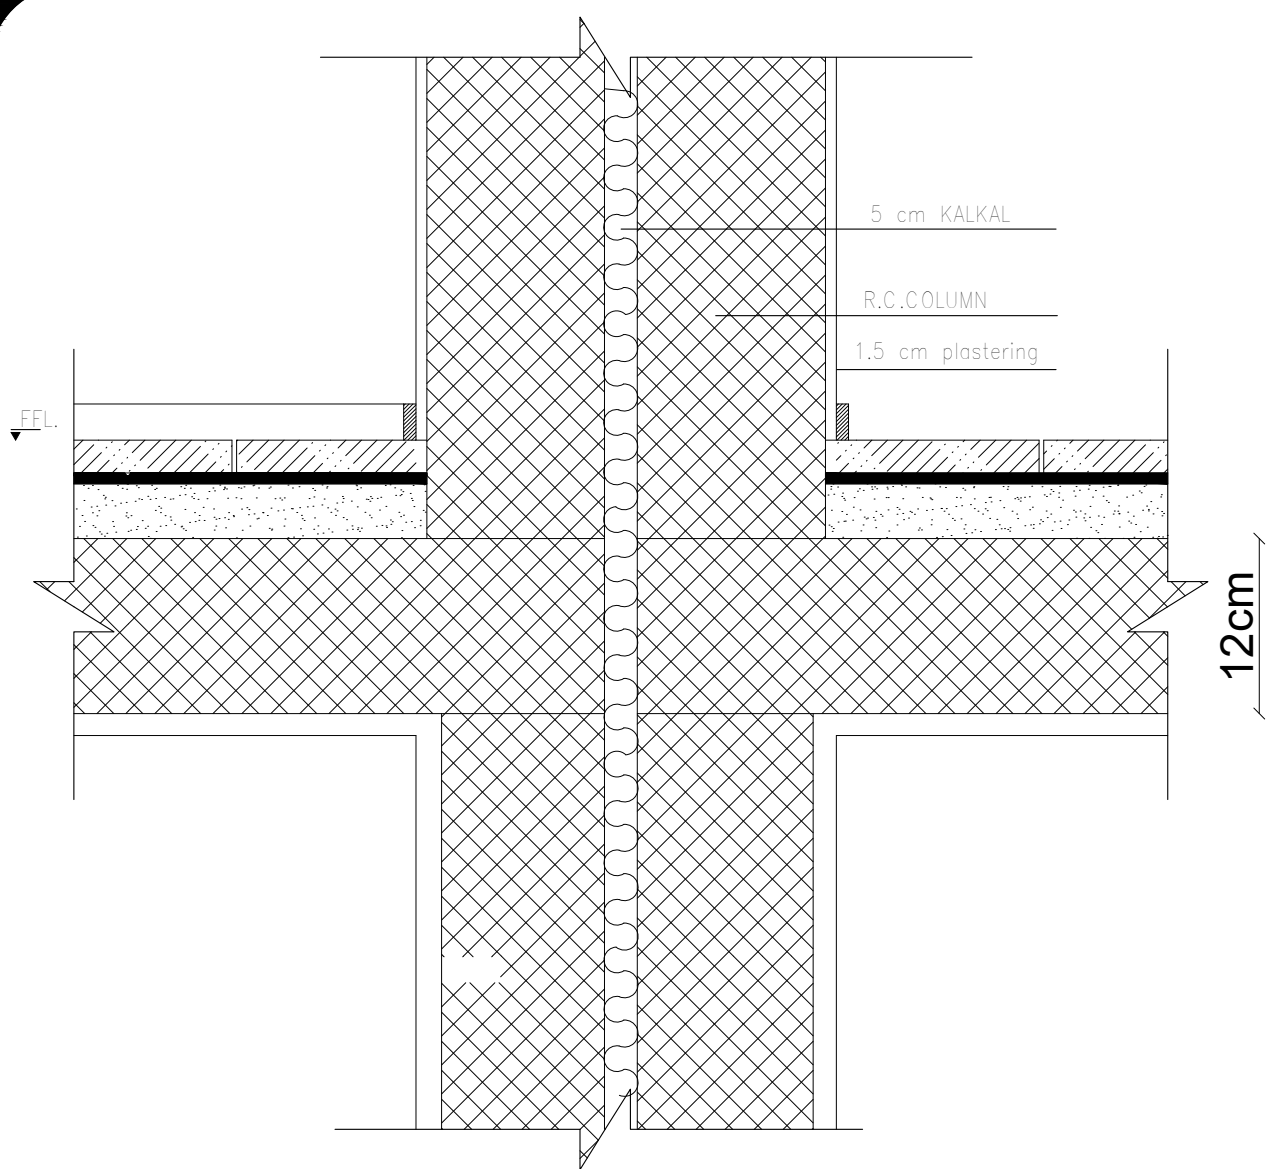

Faculty of Engineering
Cairo University
Civil Department

NOTES :

- 1- ALL DIMENSIONS AND AXES SHOULD BE READ IN CONJUNCTION WITH ARCHITECTURAL DRAWINGS BEFORE CONSTRUCTION.
- 2 - ALL DIMENSION AND LEVELS ARE IN M UNLESS OTHERWISE NOTED ON PLAN.
- 3 - THE CUBIC STRENGTH OF R. CONCRETE USED IN ALL R.C. WORKS AFTER 28 DAYS SHOULD NOT BE LESS THAN 250 Kg/cm².
- 4 - THE CEMENT USED FOR BOTH PLAIN AND REINFORCED CONCRETE UNDER GROUND LEVEL IS SULPHATE RESISTENCE PORTLAND CEMENT.
- 5 - STEEL USED IN RFT. IN R.C. WORK IS HIGH TENSILE STEEL "36/54" FOR DIAMETERS 10 mm AND MILD STEEL "24/35" FOR 8mm.
- 6 - THE REINFORCEMENT OF COULMNS WILL BE TAKEN FROM COULMNS DETAILS.
- 7 - CONCRETE COVER SHOULD NOT LESS THAN 2.5 cm FOR COULMNS.

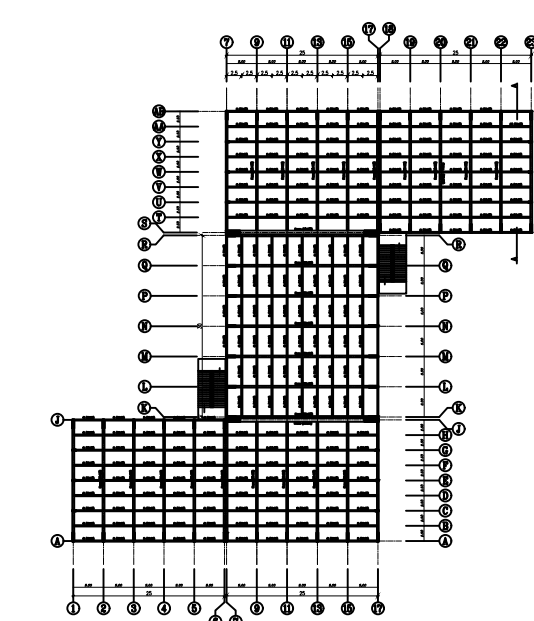

PROJECT NAME :

HALL UNIT

By :





Anas Akram Saeed

DRAWING TITLE :

FIRST FLOOR PLANE

Beam Table


Beam	Bottom Rft.		Top Rft.		Stirrups
	Main	Add.	support	mid span	
B1	2Ø16		2Ø16	2Ø10	5Ø8/m
B2	4Ø16		6Ø16	2Ø10	10Ø8/m
B3	3Ø16	-----	4Ø16	2Ø10	7Ø8/m
B4	4Ø16		3Ø16	2Ø10	5Ø8/m
B5	4Ø16		6Ø16	2Ø10	10Ø8/m
B6	2Ø16	-----	2Ø16	2Ø10	7Ø8/m
B7	2Ø16	-----	2Ø16	2Ø10	7Ø8/m

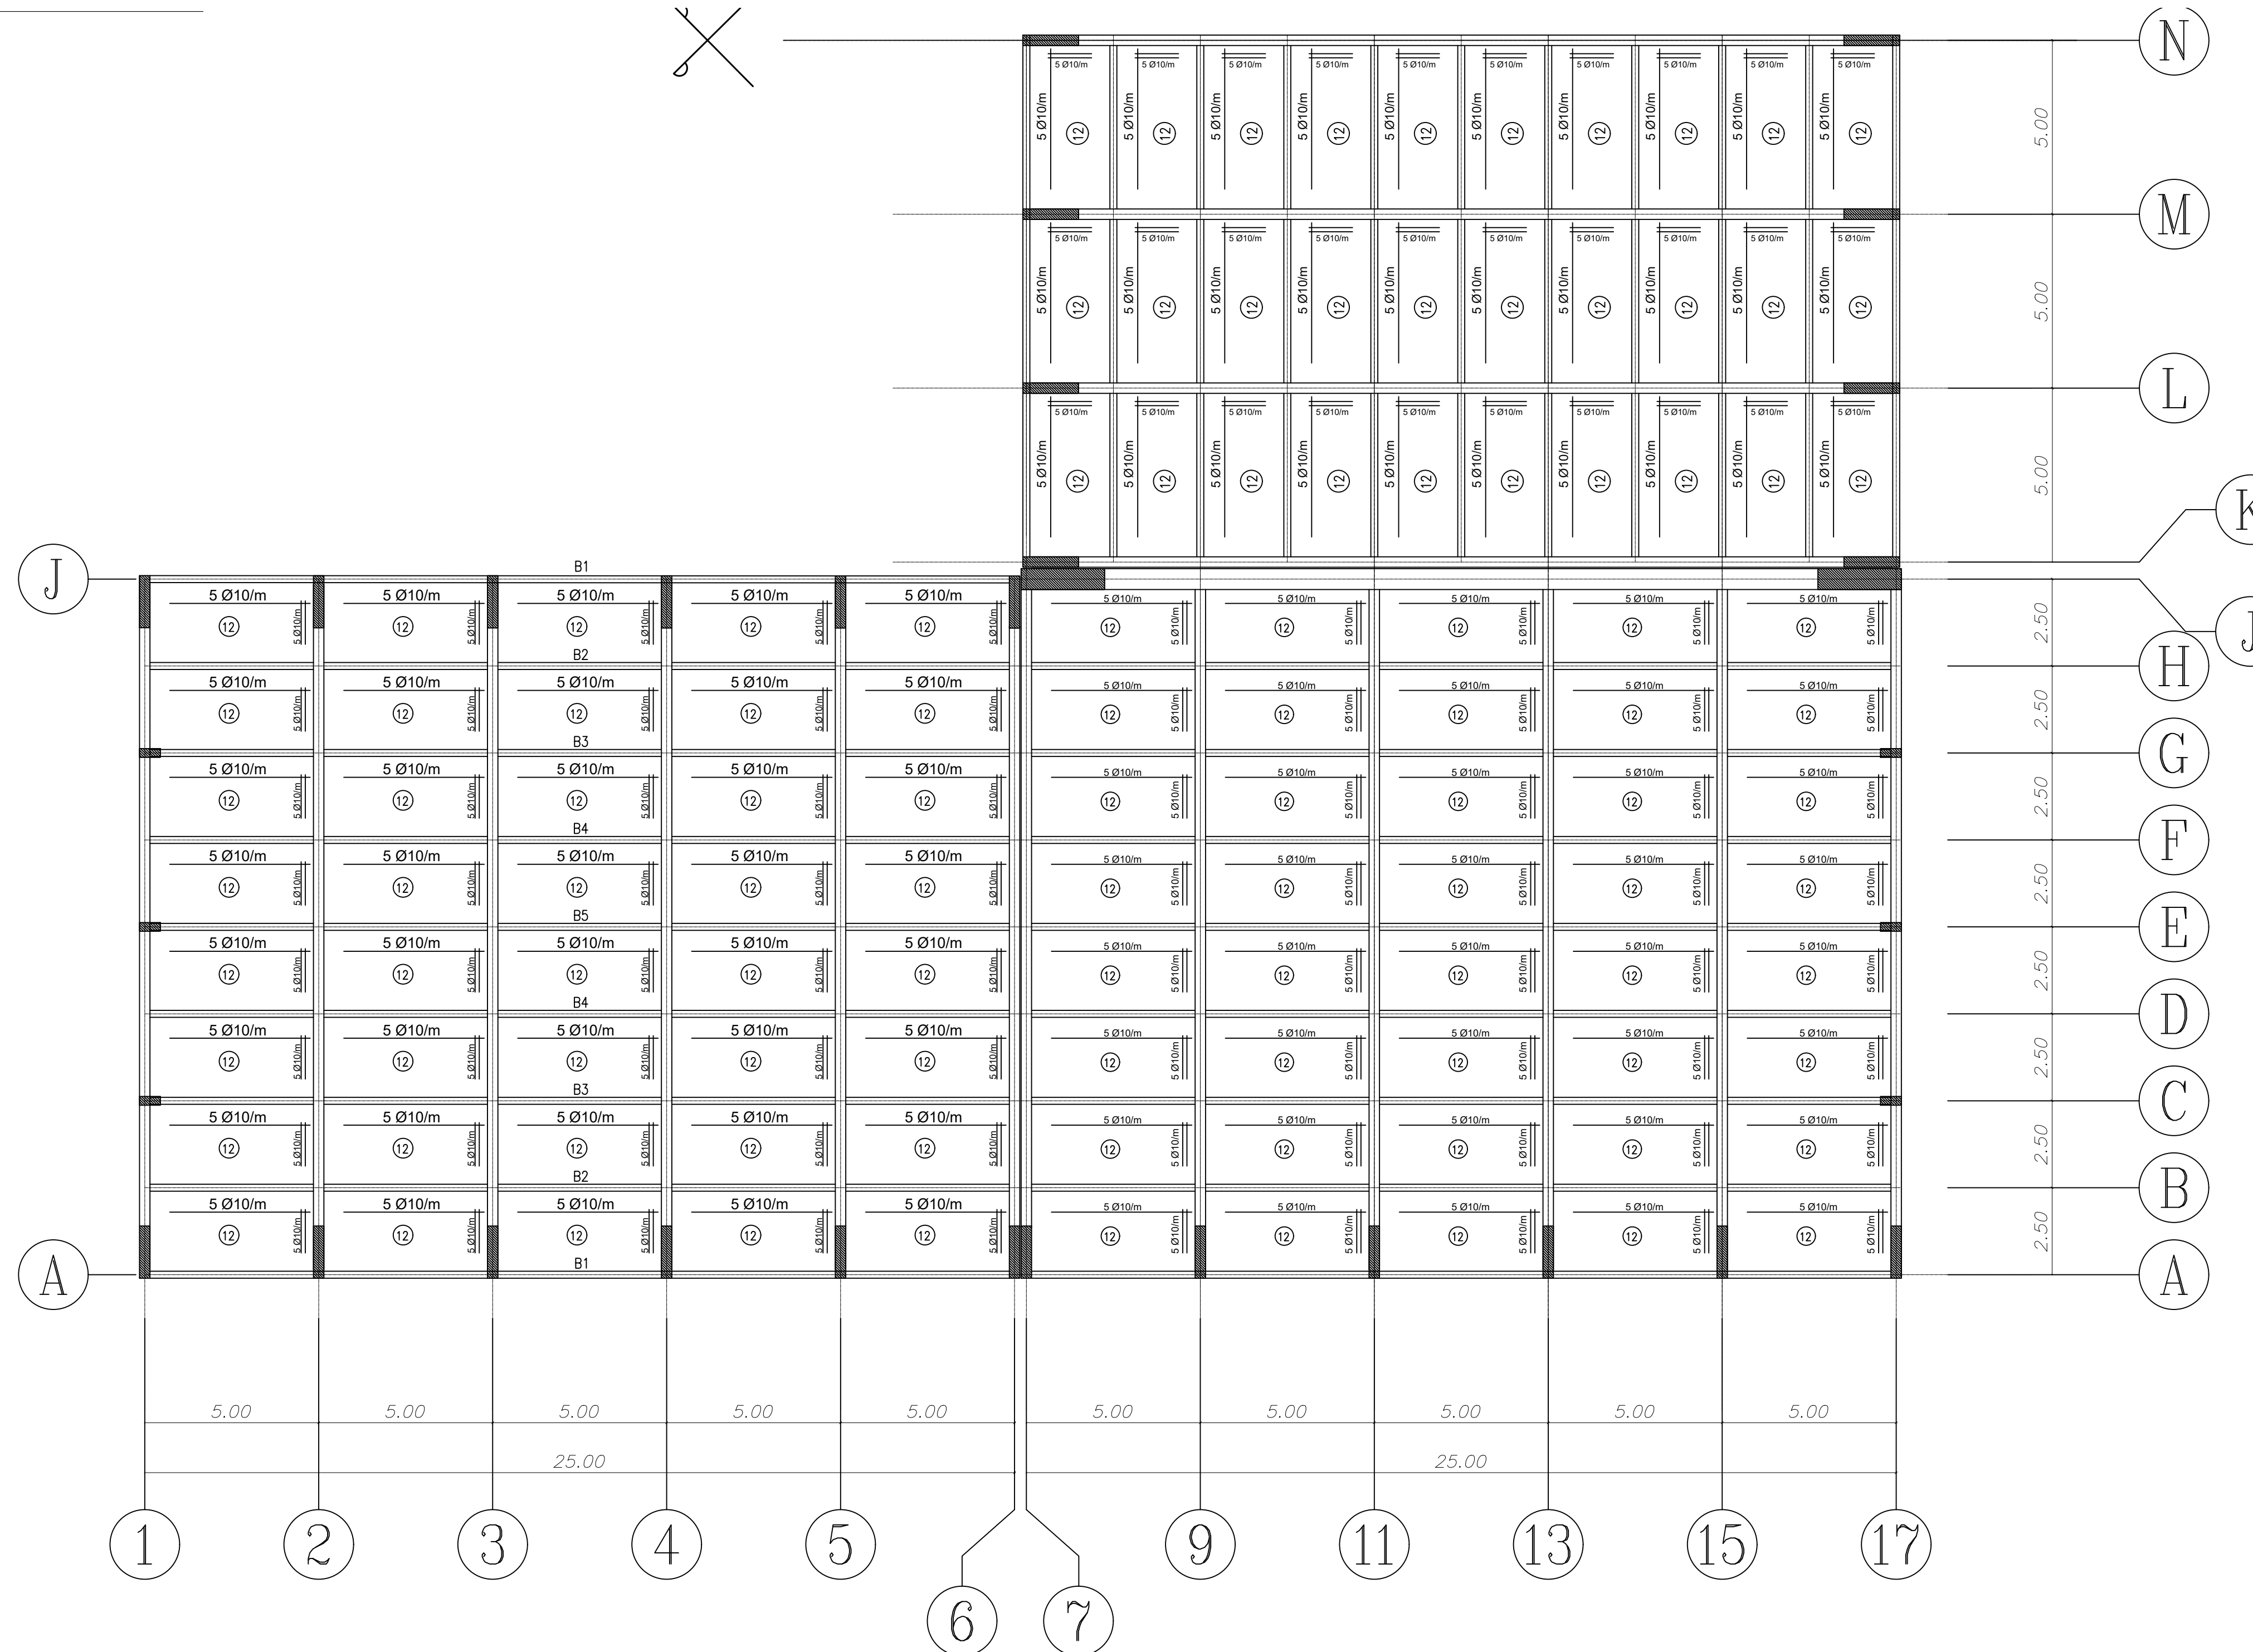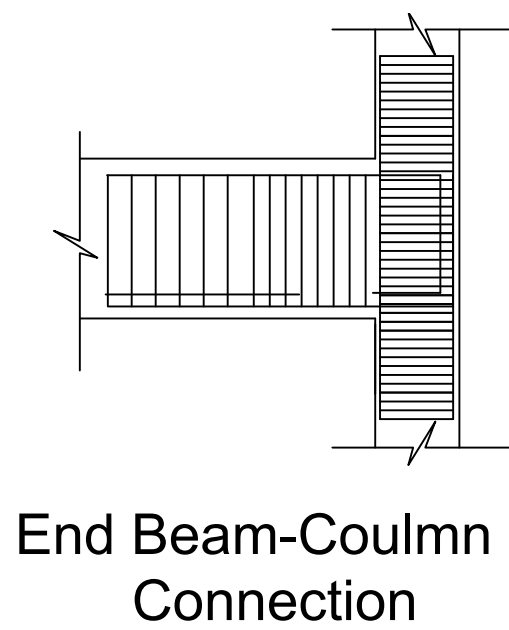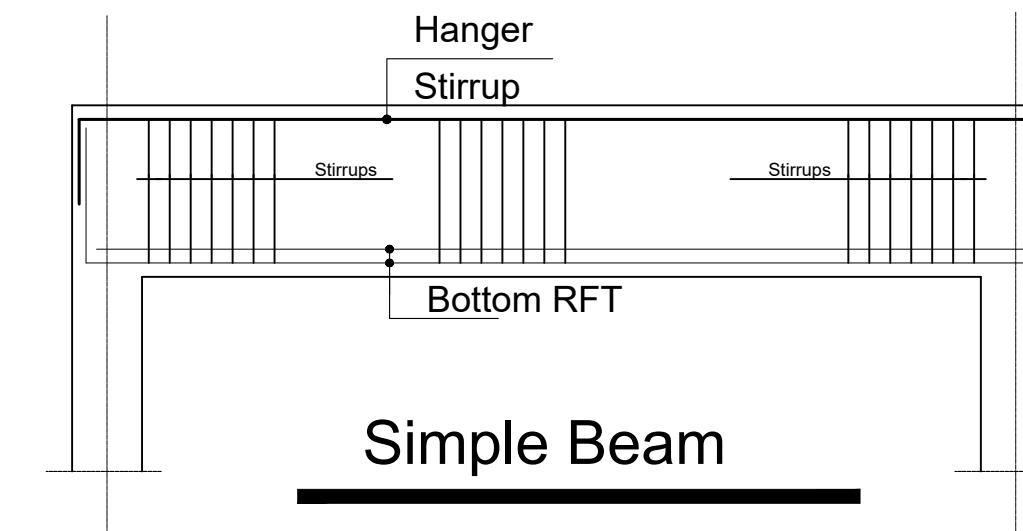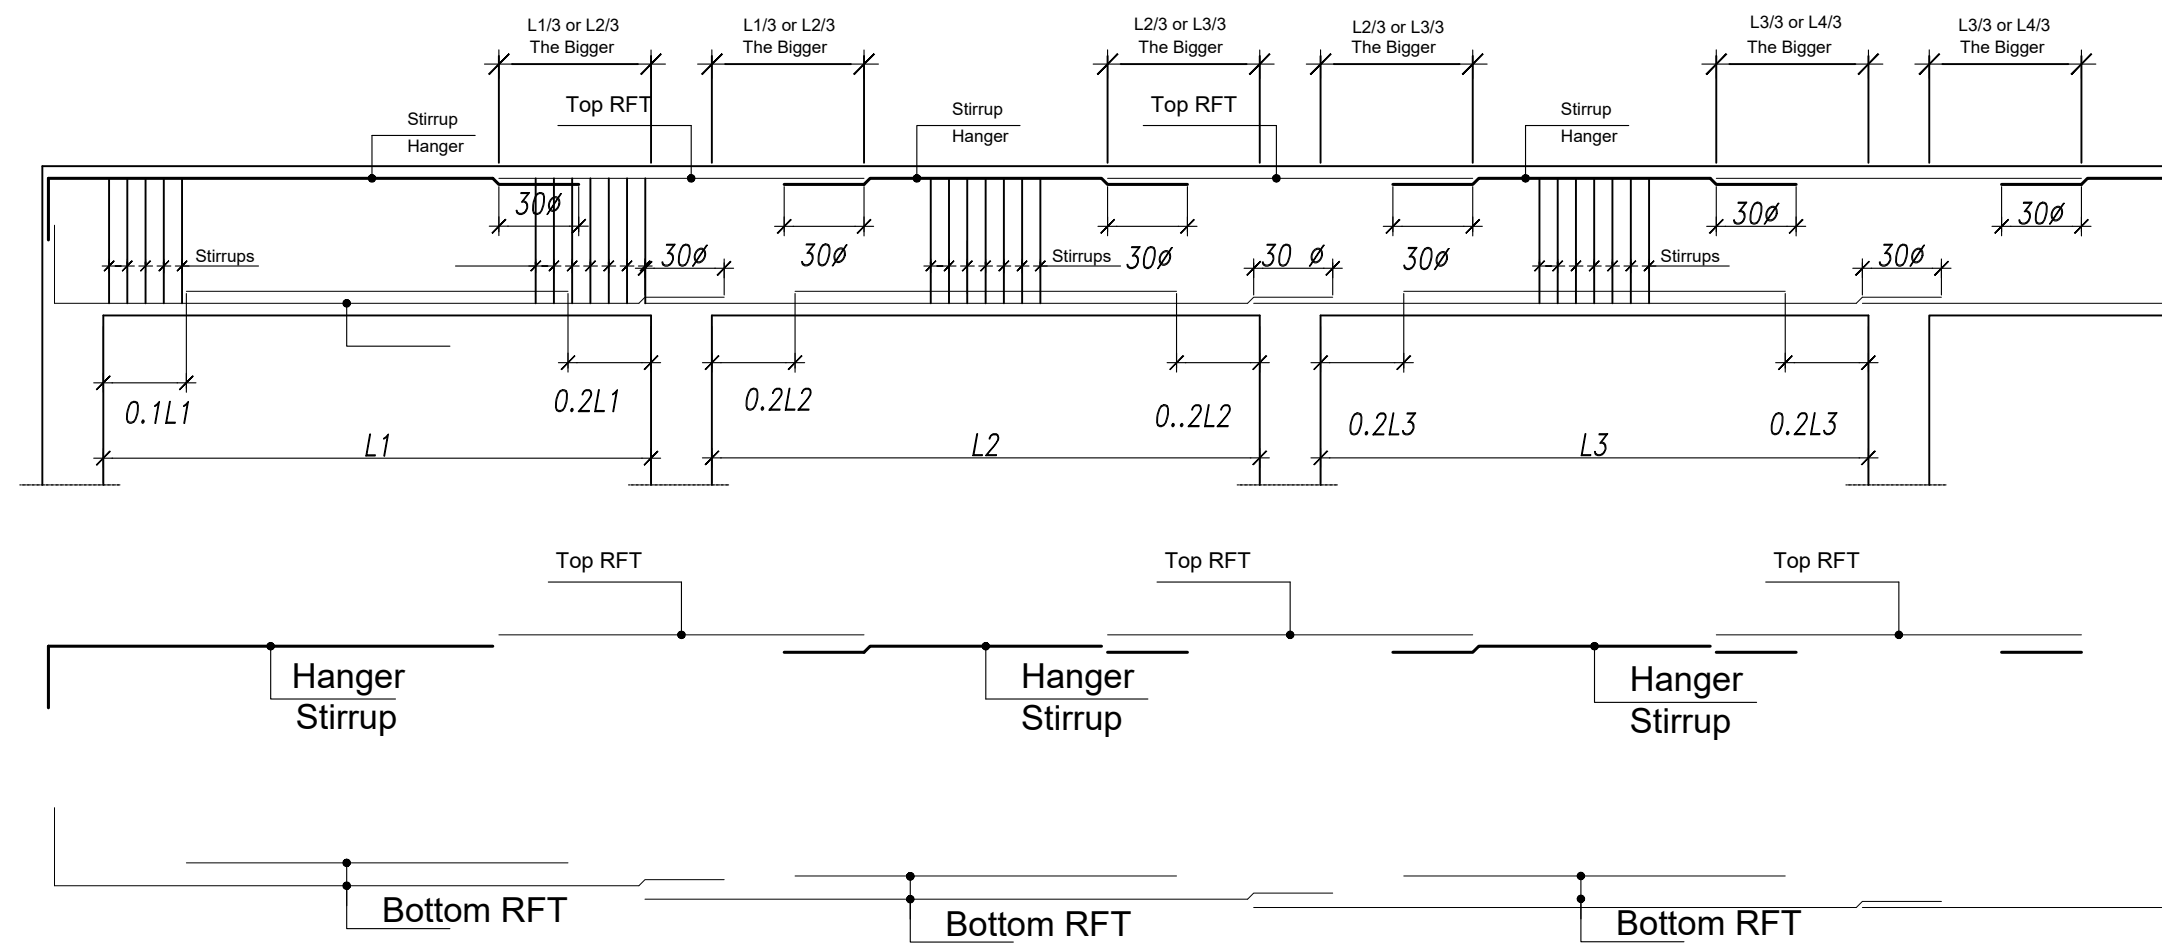

Faculty of Engineering
Cairo University
Civil Department

NOTES :

- 1- ALL DIMENSIONS AND AXES SHOULD BE READ IN CONJUNCTION WITH ARCHITECTURAL DRAWINGS BEFORE CONSTRUCTION.
- 2 - ALL DIMENSION AND LEVELS ARE IN M UNLESS OTHERWISE NOTED ON PLAN.
- 3 - THE CUBIC STRENGTH OF R. CONCRETE USED IN ALL R.C. WORKS AFTER 28 DAYS SHOULD NOT BE LESS THAN 250 Kg/cm².
- 4 - THE CEMENT USED FOR BOTH PLAIN AND REINFORCED CONCRETE UNDER GROUND LEVEL IS SULPHATE RESISTENCE PORTLAND CEMENT.
- 5 - STEEL USED IN RFT. IN R.C. WORK IS HIGH TENSILE STEEL "36/54" FOR DIAMETERS 10 mm AND MILD STEEL "24/35" FOR 8mm.
- 6 - THE REINFORCEMENT OF COULMNS WILL BE TAKEN FROM COULMNS DETAILS.
- 7 - CONCRETE COVER SHOULD NOT LESS THAN 2.5 cm FOR COULMNS.

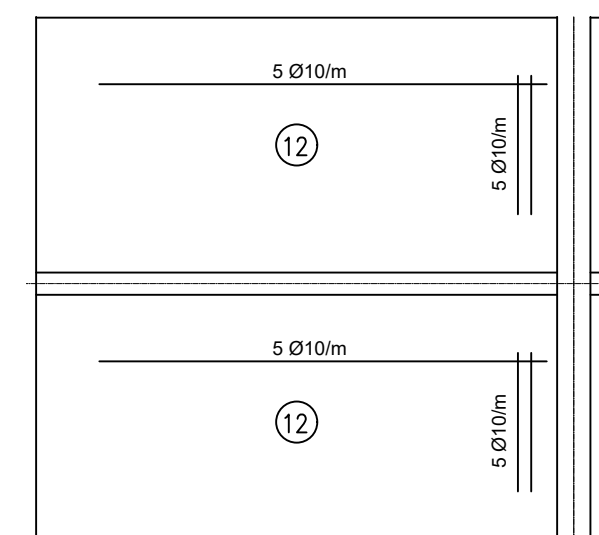

Typical Slab RFT

PROJECT NAME :

HALL UNIT

By :

Anas Akram Saeed

DRAWING TITLE :

FIRST FLOOR RFT



Faculty of Engineering
Cairo University
Civil Department

NOTES :

- 1- ALL DIMENSIONS AND AXES SHOULD BE READ IN CONJUNCTION WITH ARCHITECTURAL DRAWINGS BEFORE CONSTRUCTION.
- 2 - ALL DIMENSION AND LEVELS ARE IN M UNLESS OTHERWISE NOTED ON PLAN.
- 3 - THE CUBIC STRENGTH OF R. CONCRETE USED IN ALL R.C. WORKS AFTER 28 DAYS SHOULD NOT BE LESS THAN 250 Kg/cm² .
- 4 - THE CEMENT USED FOR BOTH PLAIN AND REINFORCED CONCRETE UNDER GROUND LEVEL IS SULPHATE RESISTENCE PORTLAND CEMENT.
- 5 - STEEL USED IN RFT. IN R.C. WORK IS HIGH TENSILE STEEL "36/54" FOR DIAMETERS 10 mm AND MILD STEEL "24/35" FOR 8mm.
- 6 - THE REINFORCEMENT OF COULMNS WILL BE TAKEN FROM COULMNS DETAILS.
- 7 - CONCRETE COVER SHOULD NOT LESS THAN 2.5 cm FOR COULMNS.

PROJECT NAME :


HALL UNIT

By :


Anas Akram Saeed

DRAWING TITLE :


Frame Span 25m RFT

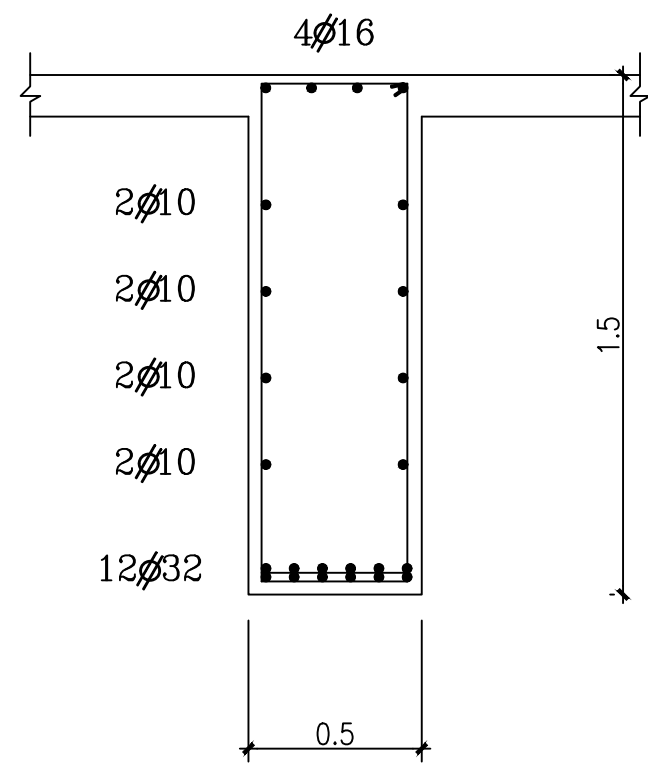


Section 1-1

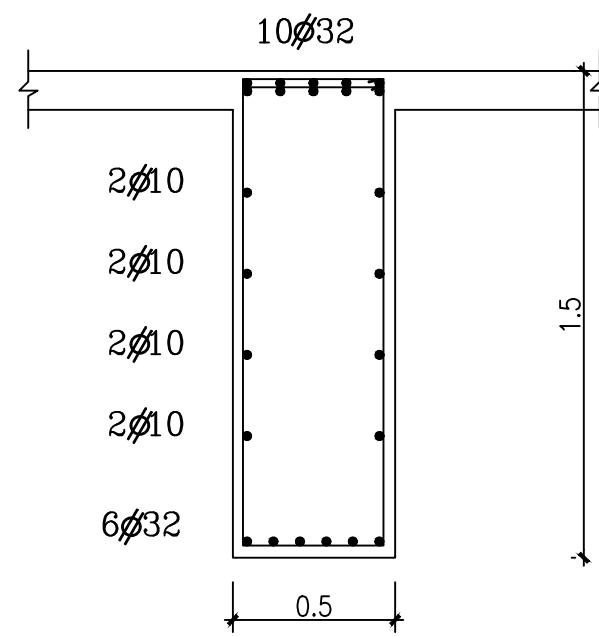

Section 2-2

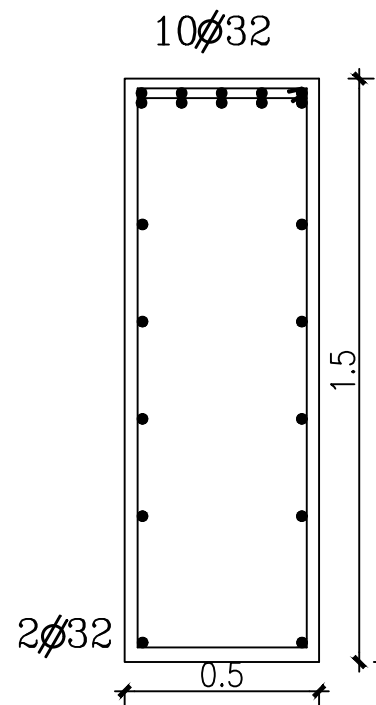

Section 3-3

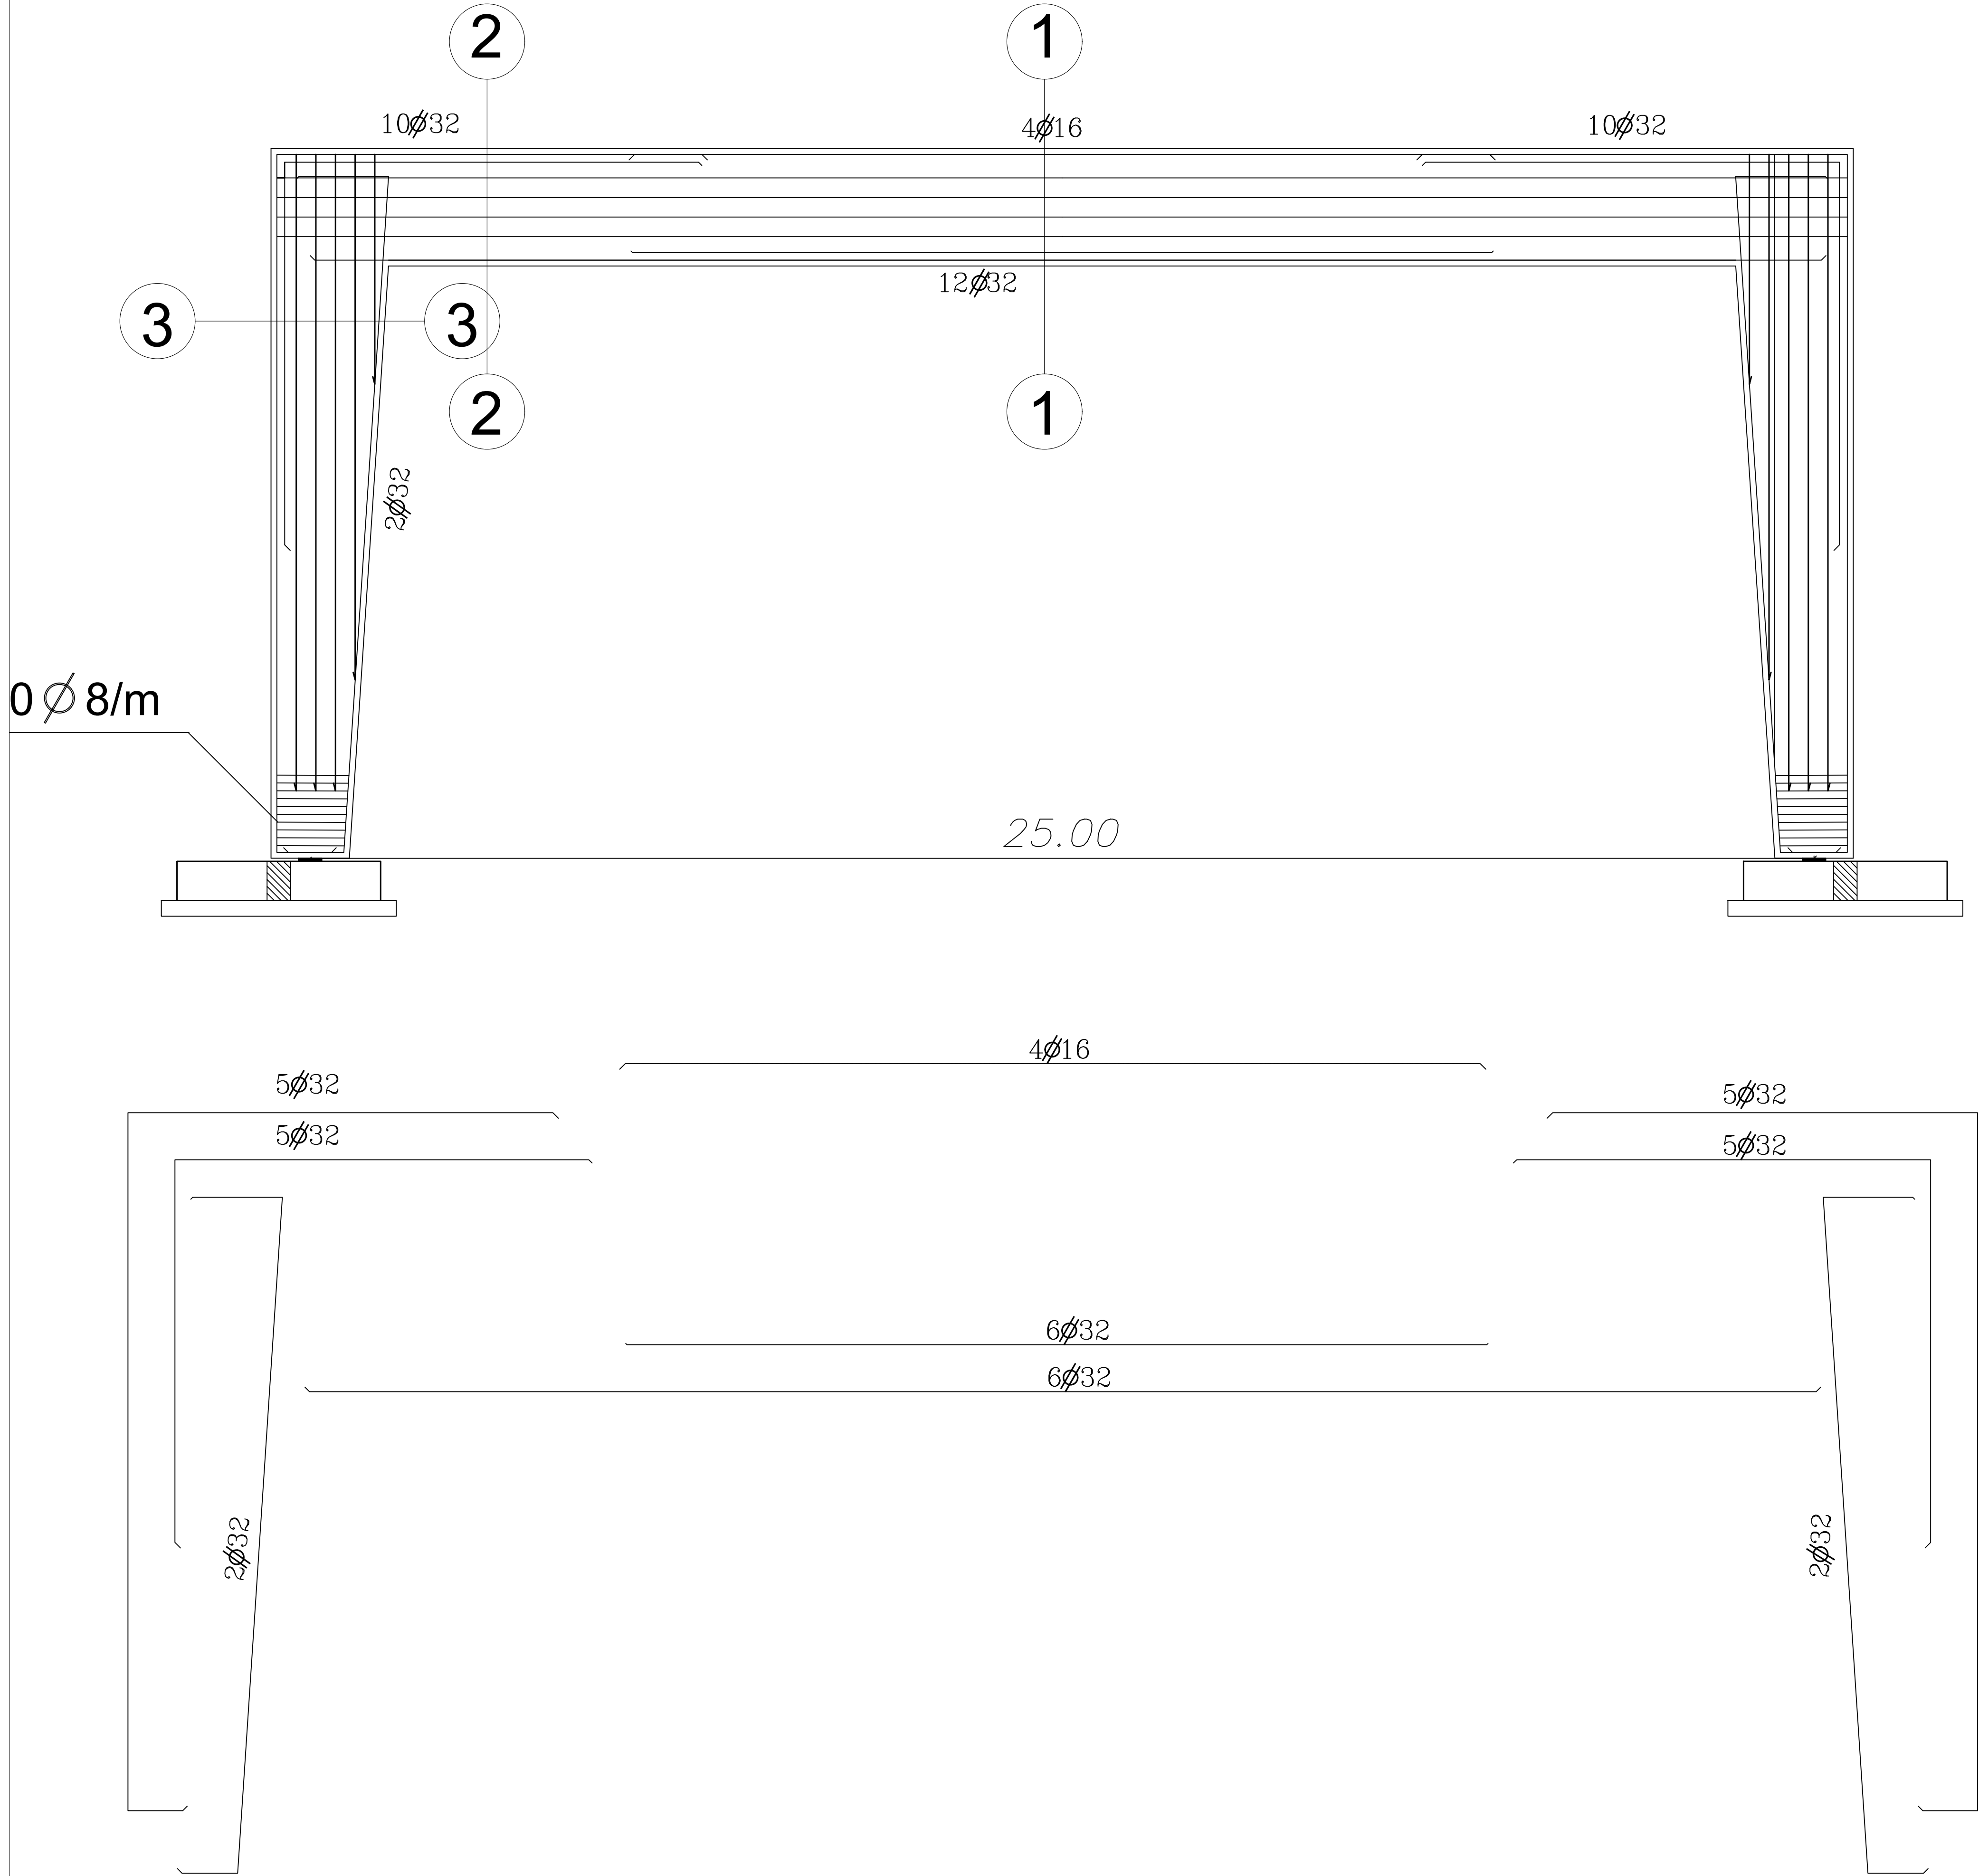



NOTES :

- 1 - ALL DIMENSIONS AND AXES SHOULD BE READ IN CONJUNCTION WITH ARCHITECTURAL DRAWINGS BEFORE CONSTRUCTION.
- 2 - ALL DIMENSION AND LEVELS ARE IN M UNLESS OTHERWISE NOTED ON PLAN.
- 3 - THE CUBIC STRENGTH OF R. CONCRETE USED IN ALL R.C. WORKS AFTER 28 DAYS SHOULD NOT BE LESS THAN 250 Kg/cm² .
- 4 - THE CEMENT USED FOR BOTH PLAIN AND REINFORCED CONCRETE UNDER GROUND LEVEL IS SULPHATE RESISTENCE PORTLAND CEMENT.
- 5 - STEEL USED IN RFT. IN R.C. WORK IS HIGH TENSILE STEEL "36/54" FOR DIAMETERS 10 mm AND MILD STEEL "24/35" FOR 8mm.
- 6 - THE REINFORCEMENT OF COULMNS WILL BE TAKEN FROM COULMNS DETAILS.
- 7 - CONCRETE COVER SHOULD NOT LESS THAN 2.5 cm FOR COULMNS.

PROJECT NAME :


HALL UNIT

By :


Anas Akram Saeed

DRAWING TITLE :


Frame Span 20m RFT

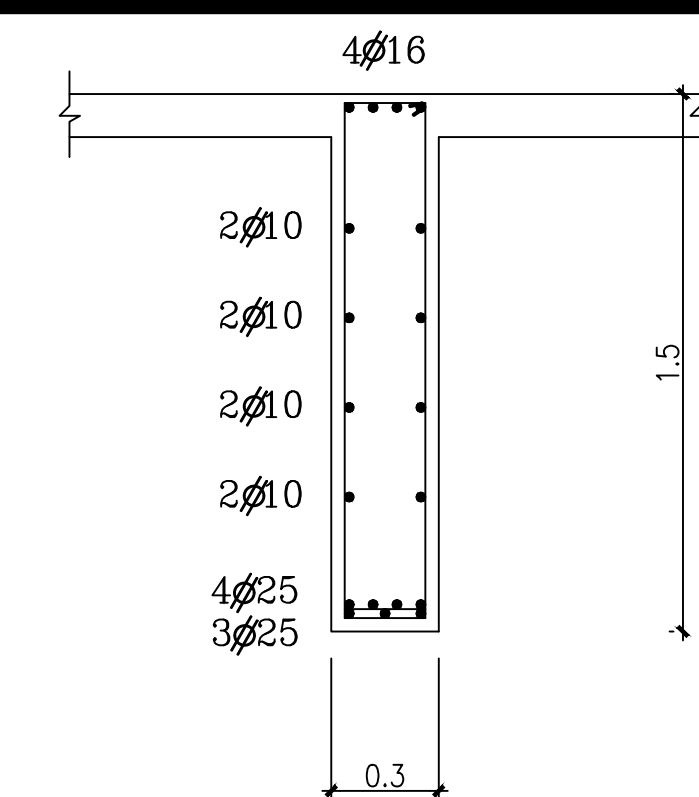


Section 1-1

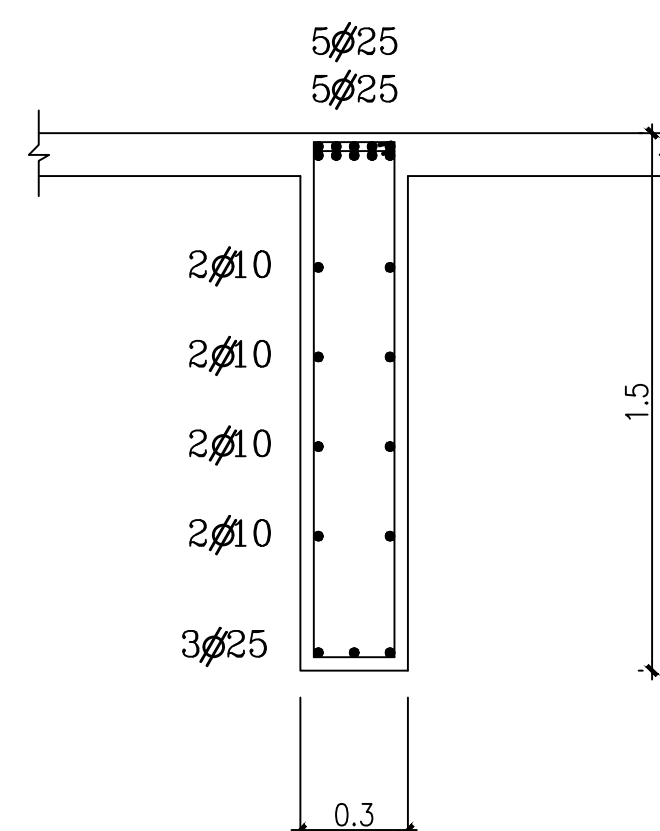


Section 2-2

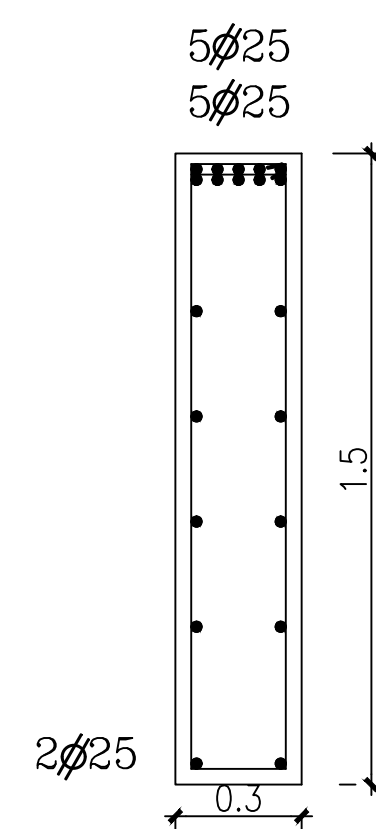

Section 3-3

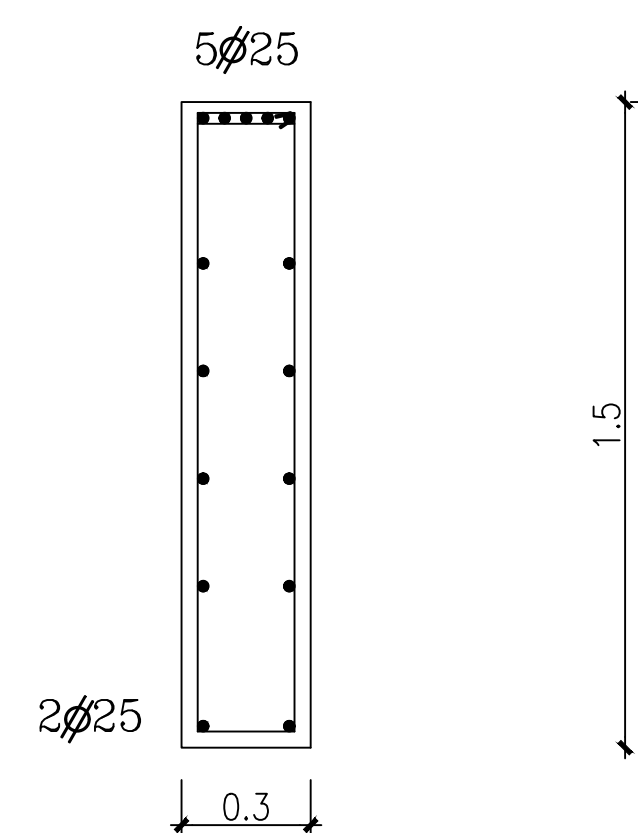

Section 4-4

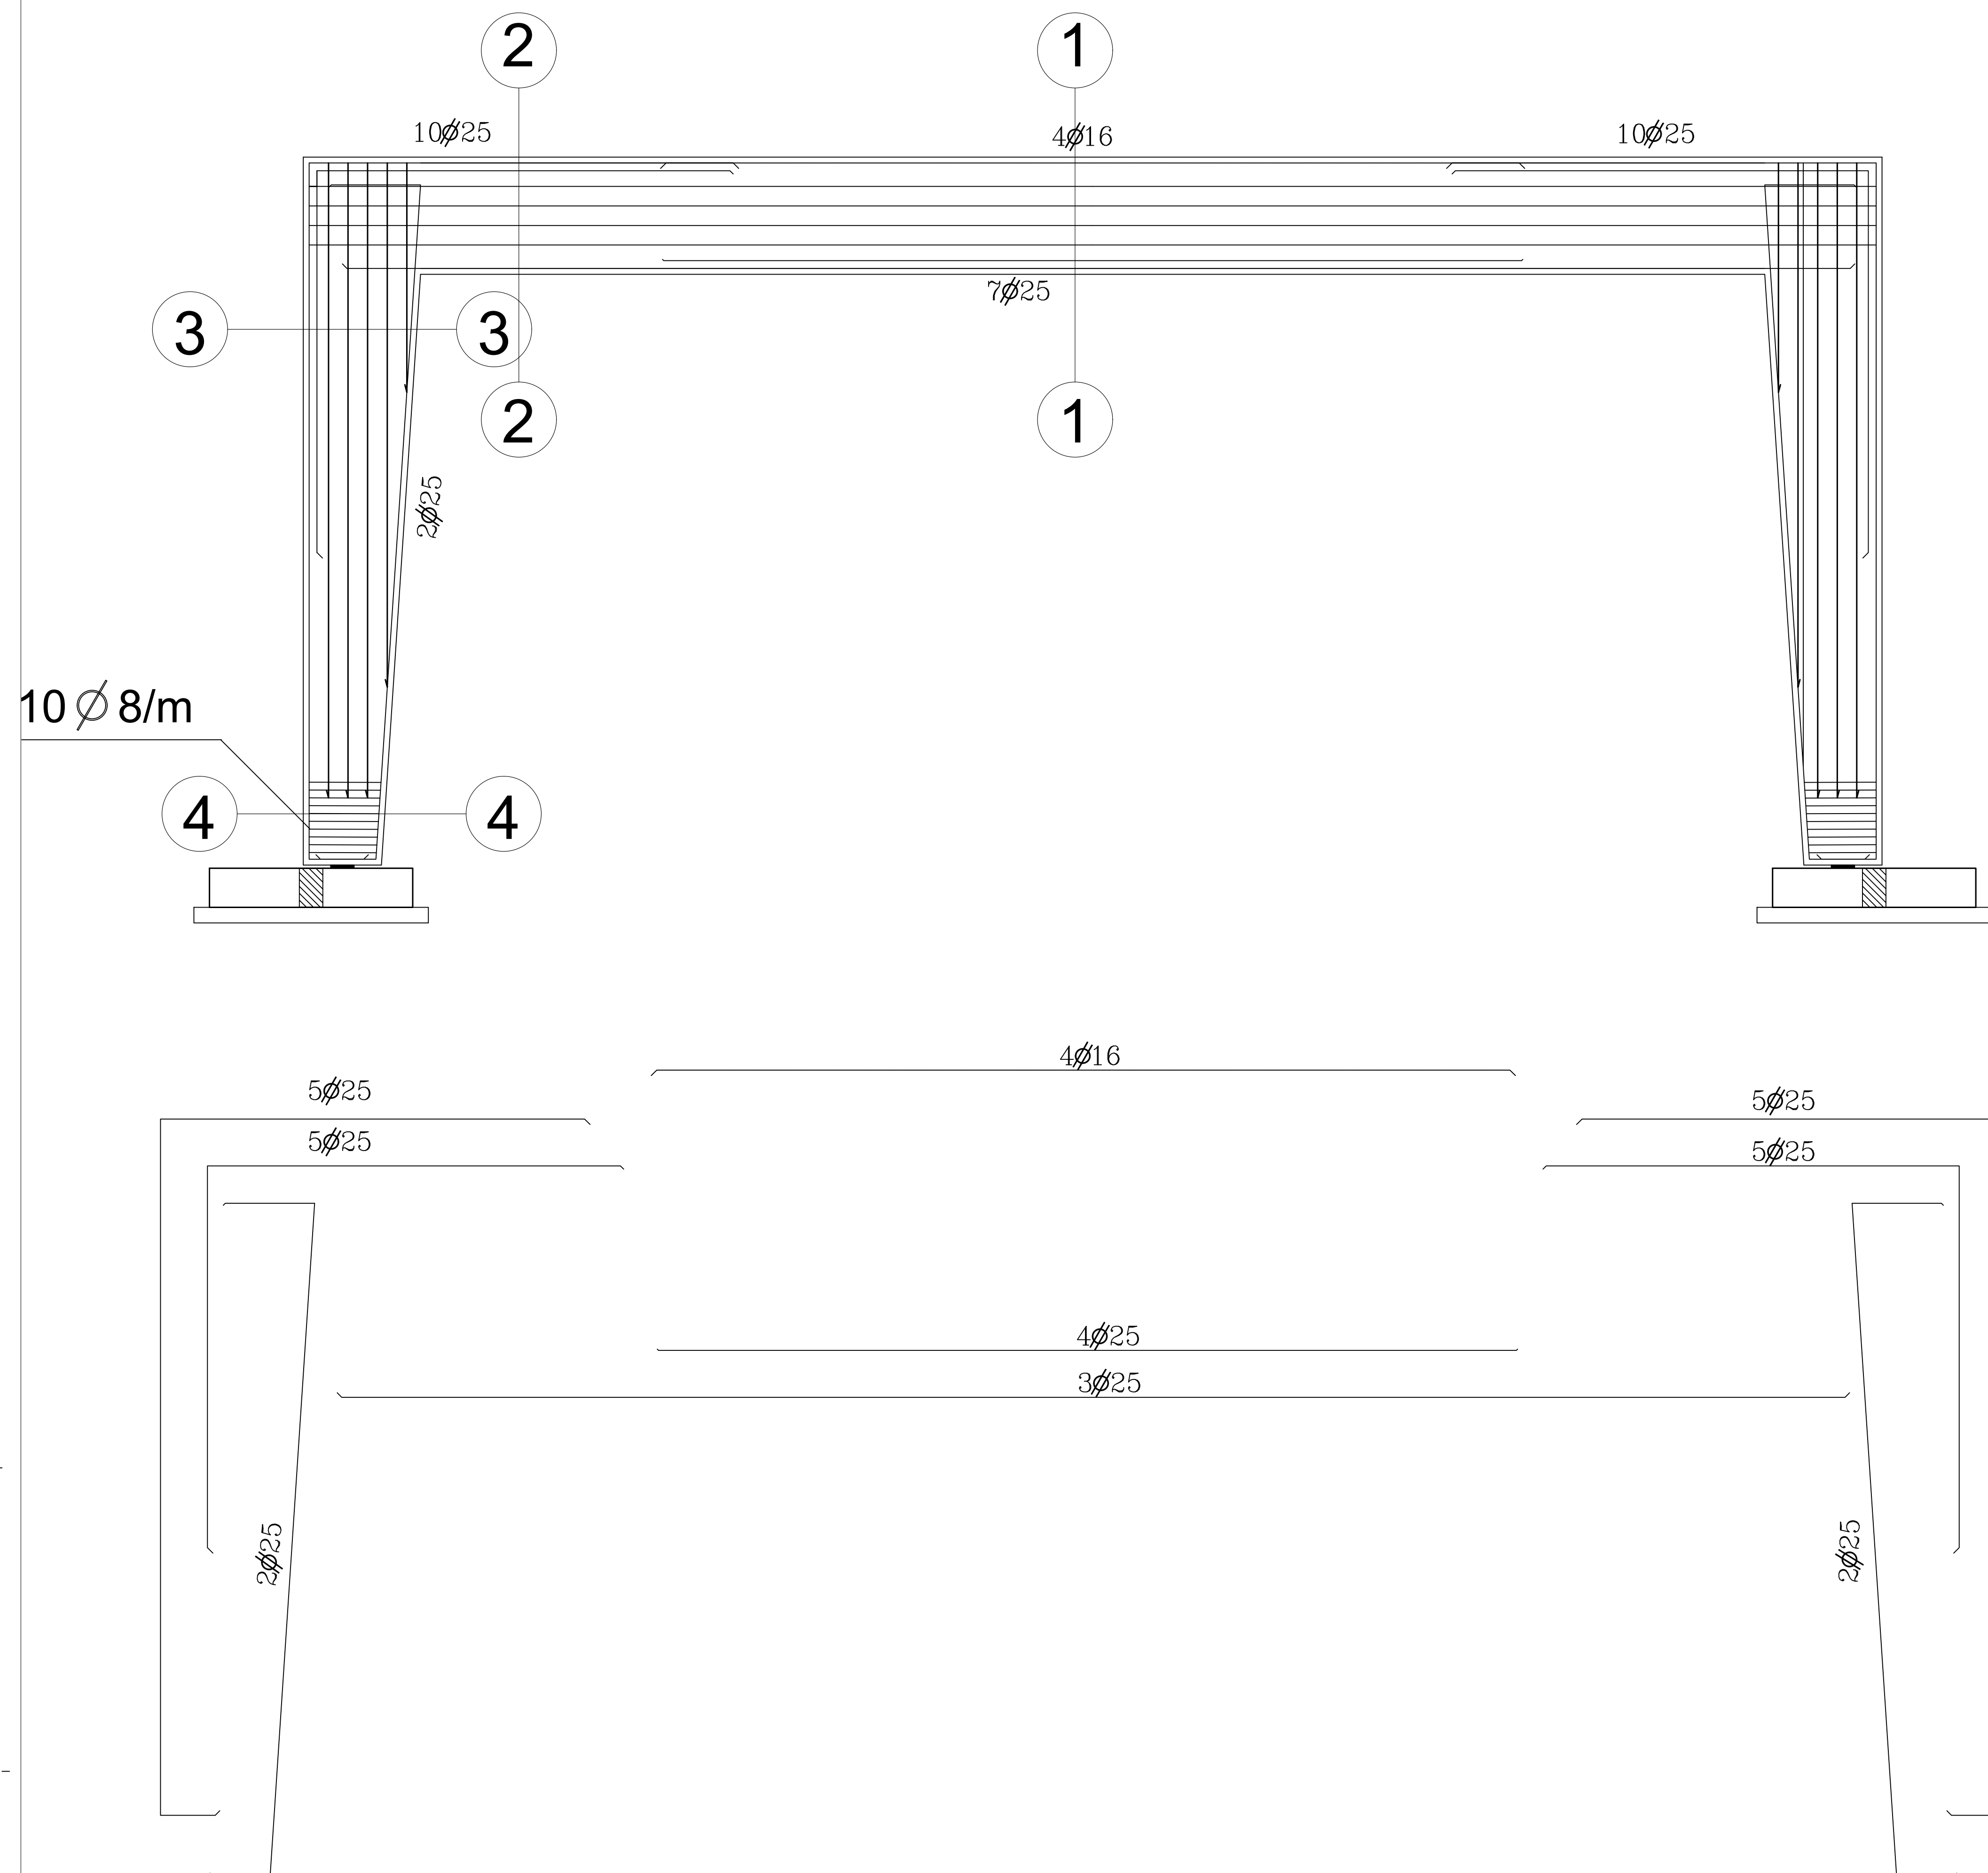



Faculty of Engineering
Cairo University
Civil Department

NOTES :

- 1- ALL DIMENSIONS AND AXES SHOULD BE READ IN CONJUNCTION WITH ARCHITECTURAL DRAWINGS BEFORE CONSTRUCTION.
- 2 - ALL DIMENSION AND LEVELS ARE IN M UNLESS OTHERWISE NOTED ON PLAN.
- 3 - THE CUBIC STRENGTH OF R. CONCRETE USED IN ALL R.C. WORKS AFTER 28 DAYS SHOULD NOT BE LESS THAN 250 Kg/cm².
- 4 - THE CEMENT USED FOR BOTH PLAIN AND REINFORCED CONCRETE UNDER GROUND LEVEL IS SULPHATE RESISTENCE PORTLAND CEMENT.
- 5 - STEEL USED IN RFT. IN R.C. WORK IS HIGH TENSILE STEEL "36/54" FOR DIAMETERS 10 mm AND MILD STEEL "24/35" FOR 8mm.
- 6 - THE REINFORCEMENT OF COULMNS WILL BE TAKEN FROM COULMNS DETAILS.
- 7 - CONCRETE COVER SHOULD NOT LESS THAN 2.5 cm FOR COULMNS.
- 8 - DESIGN IS CARRIED TO THE REQUIREMENTS OF THE EGYPTION CODE OF PRACTICE (2020).
- 9 - CONCRETE USED SHOULD BE VERY DENSE AND CURING MUST BE ACCORDING TO EGYPTIAN CODE OF PRACTICE (2020).

PROJECT NAME :


HALL UNIT

By :


Anas Akram Saeed

DRAWING TITLE :


Folded Plate RFT

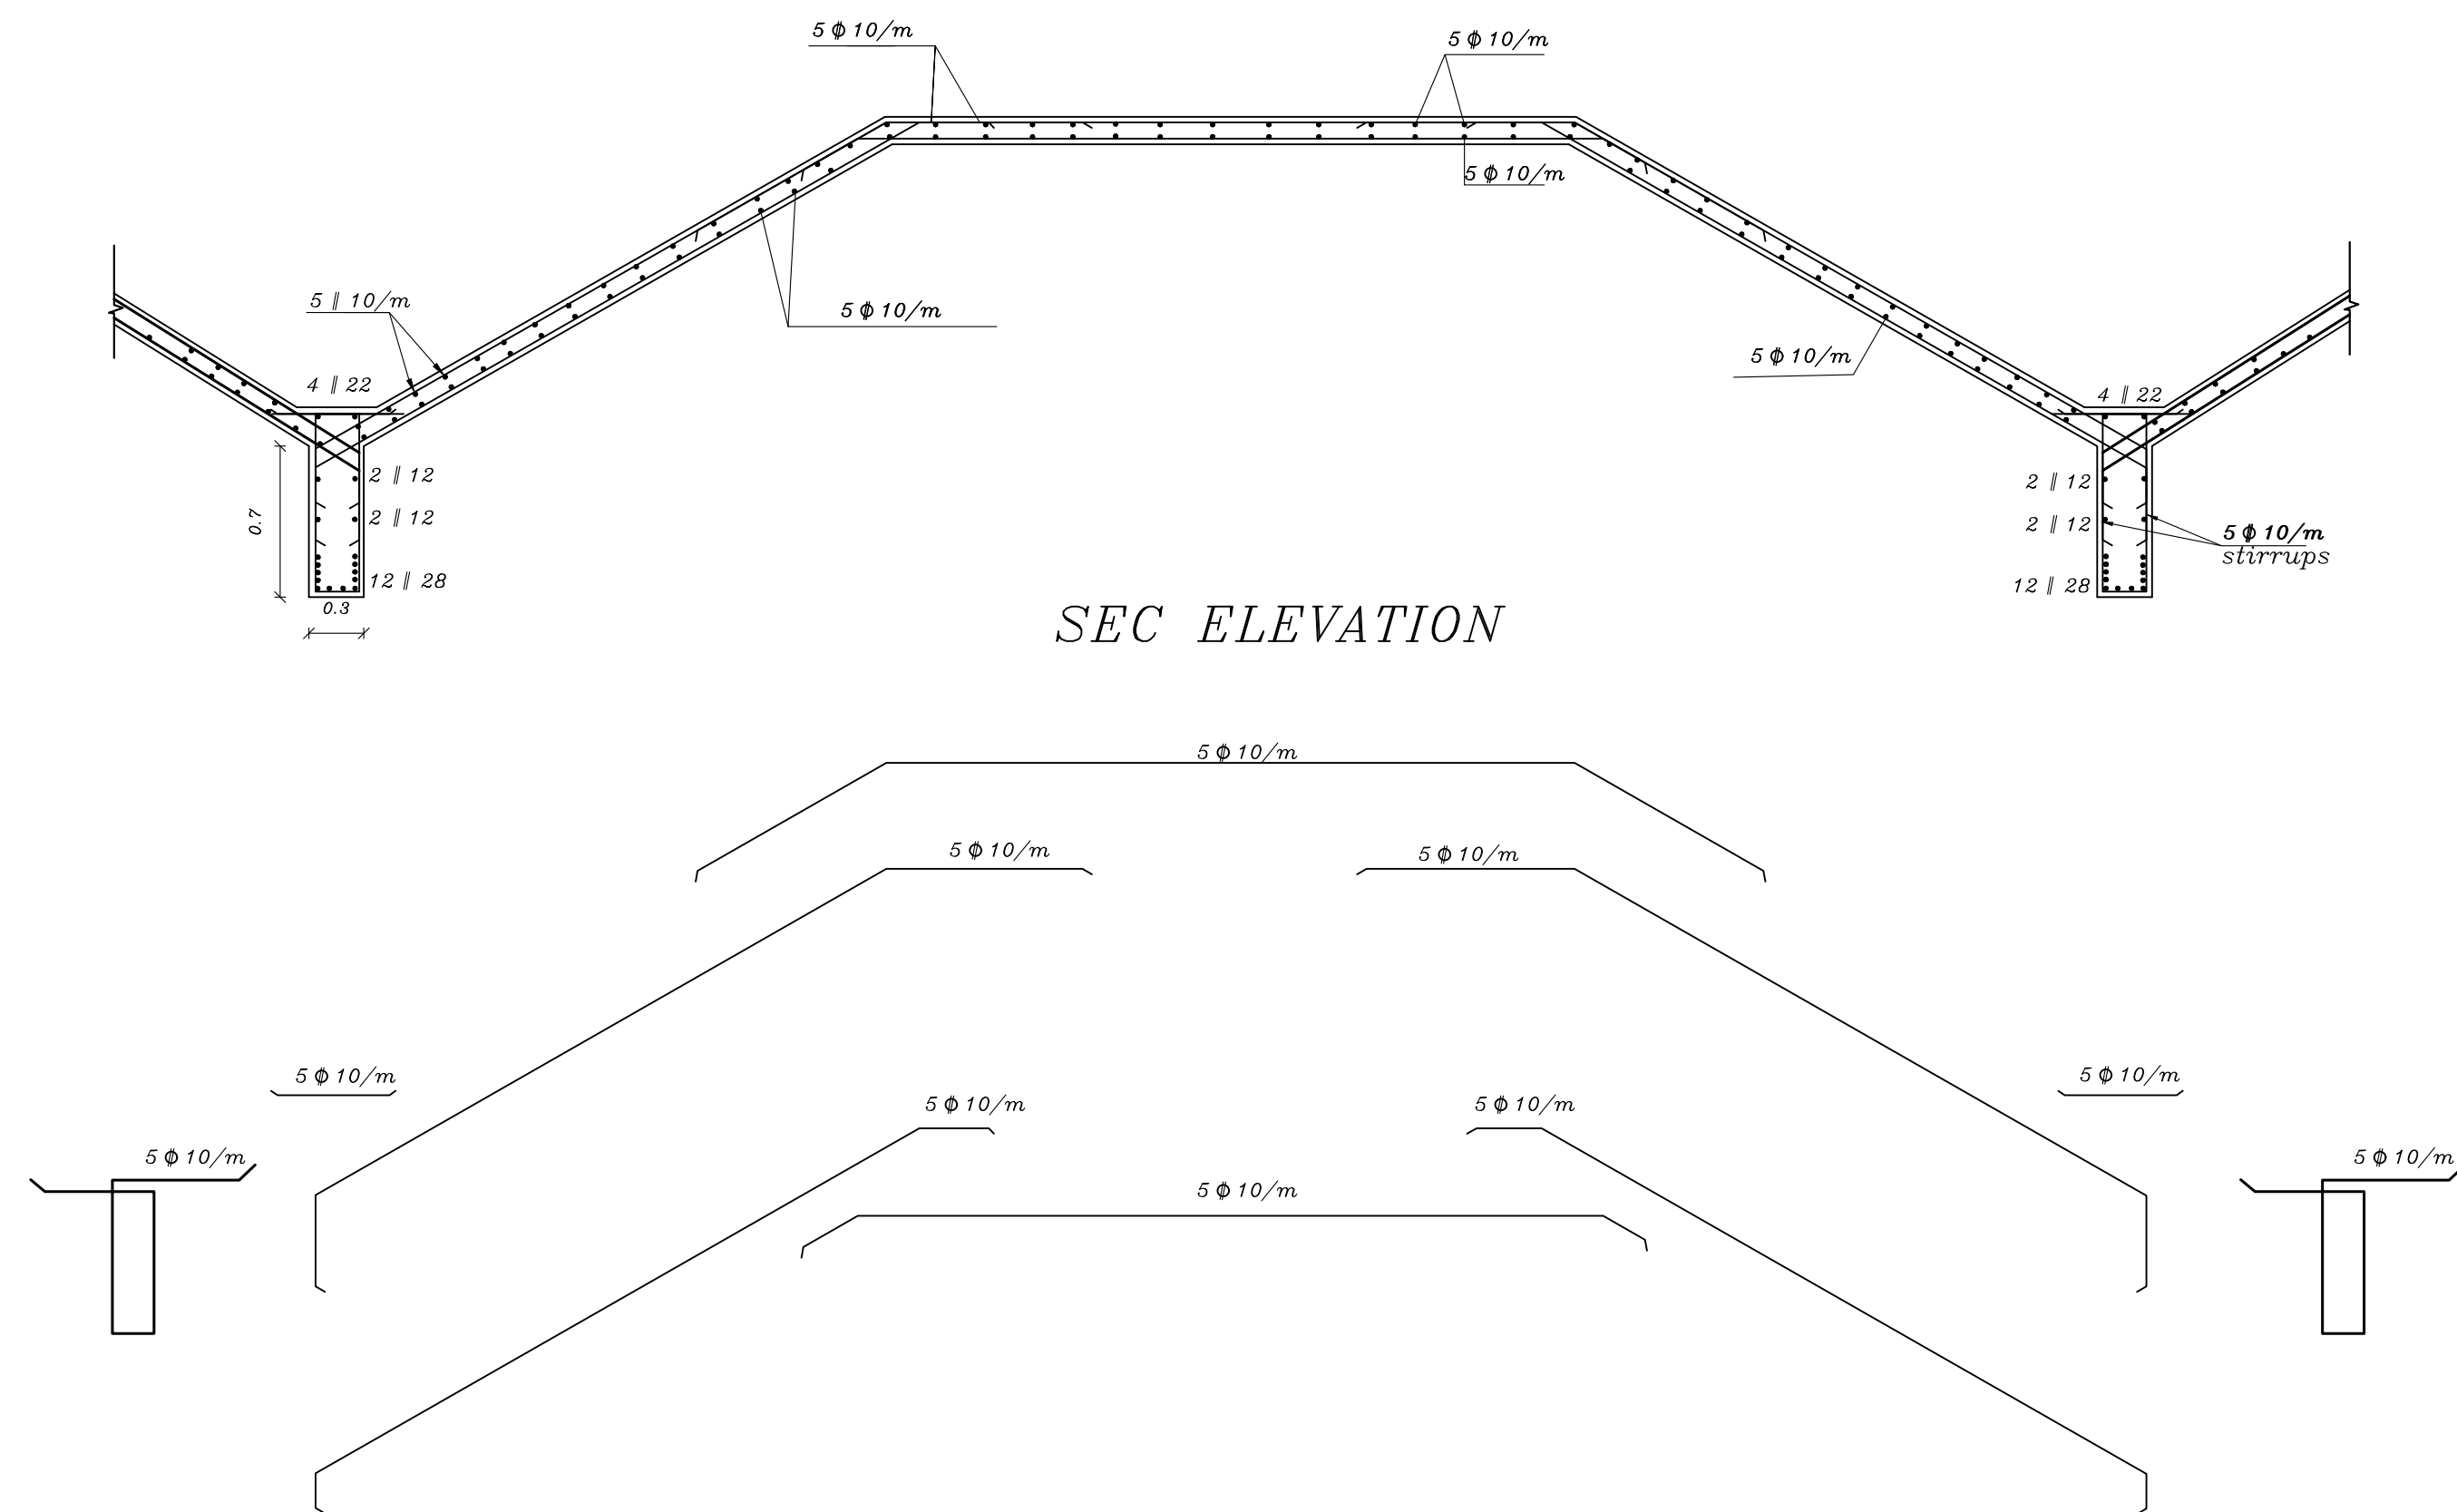


SEC ELEVATION

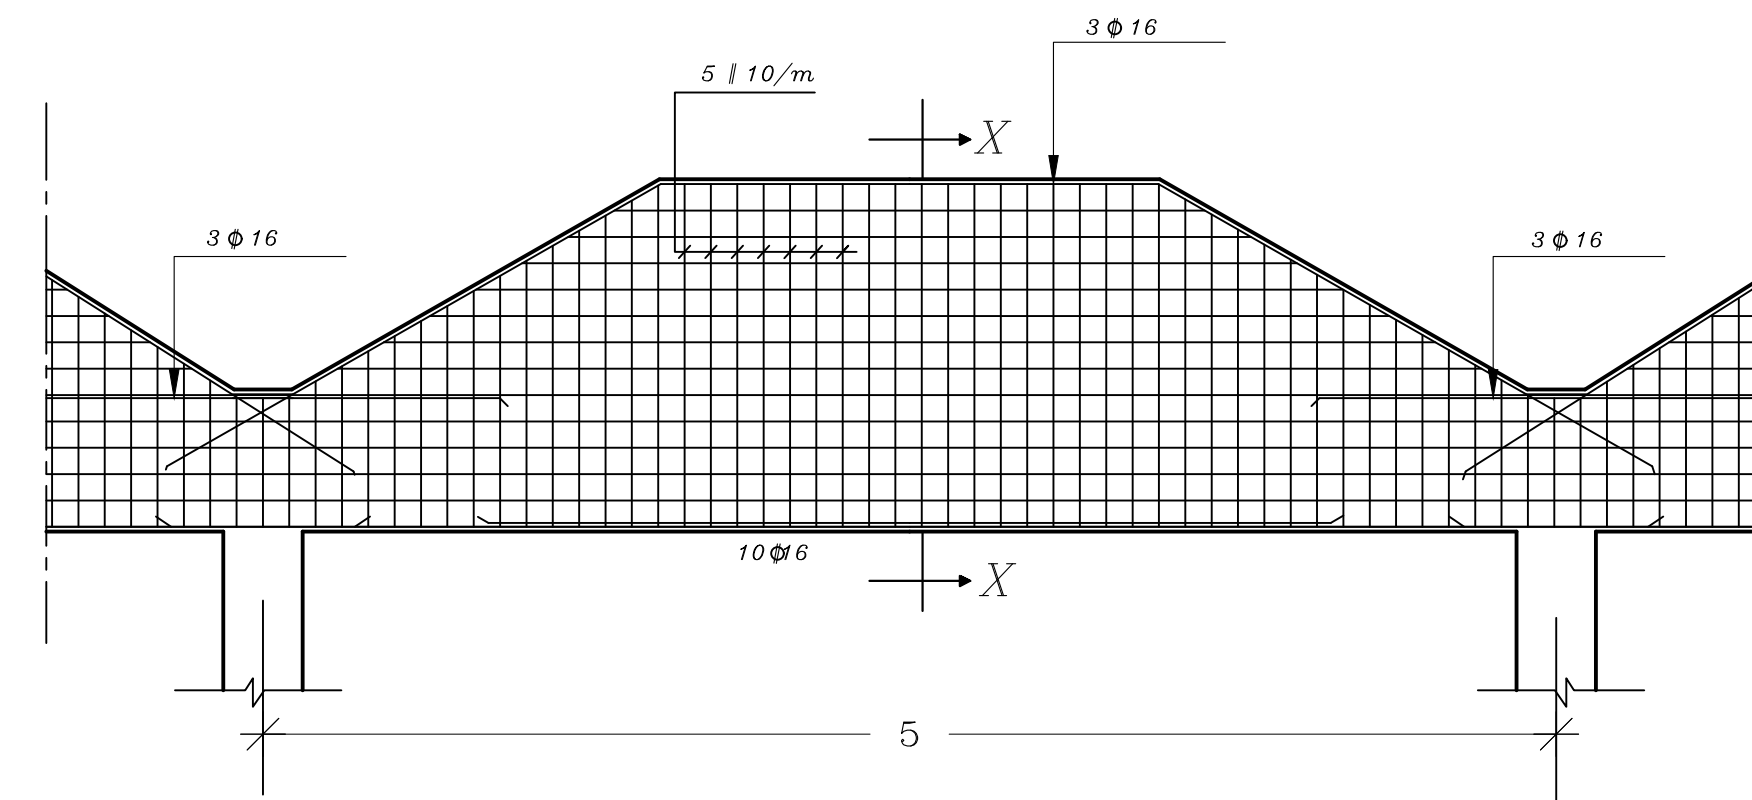

DETAILS OF DIAPHRAGM

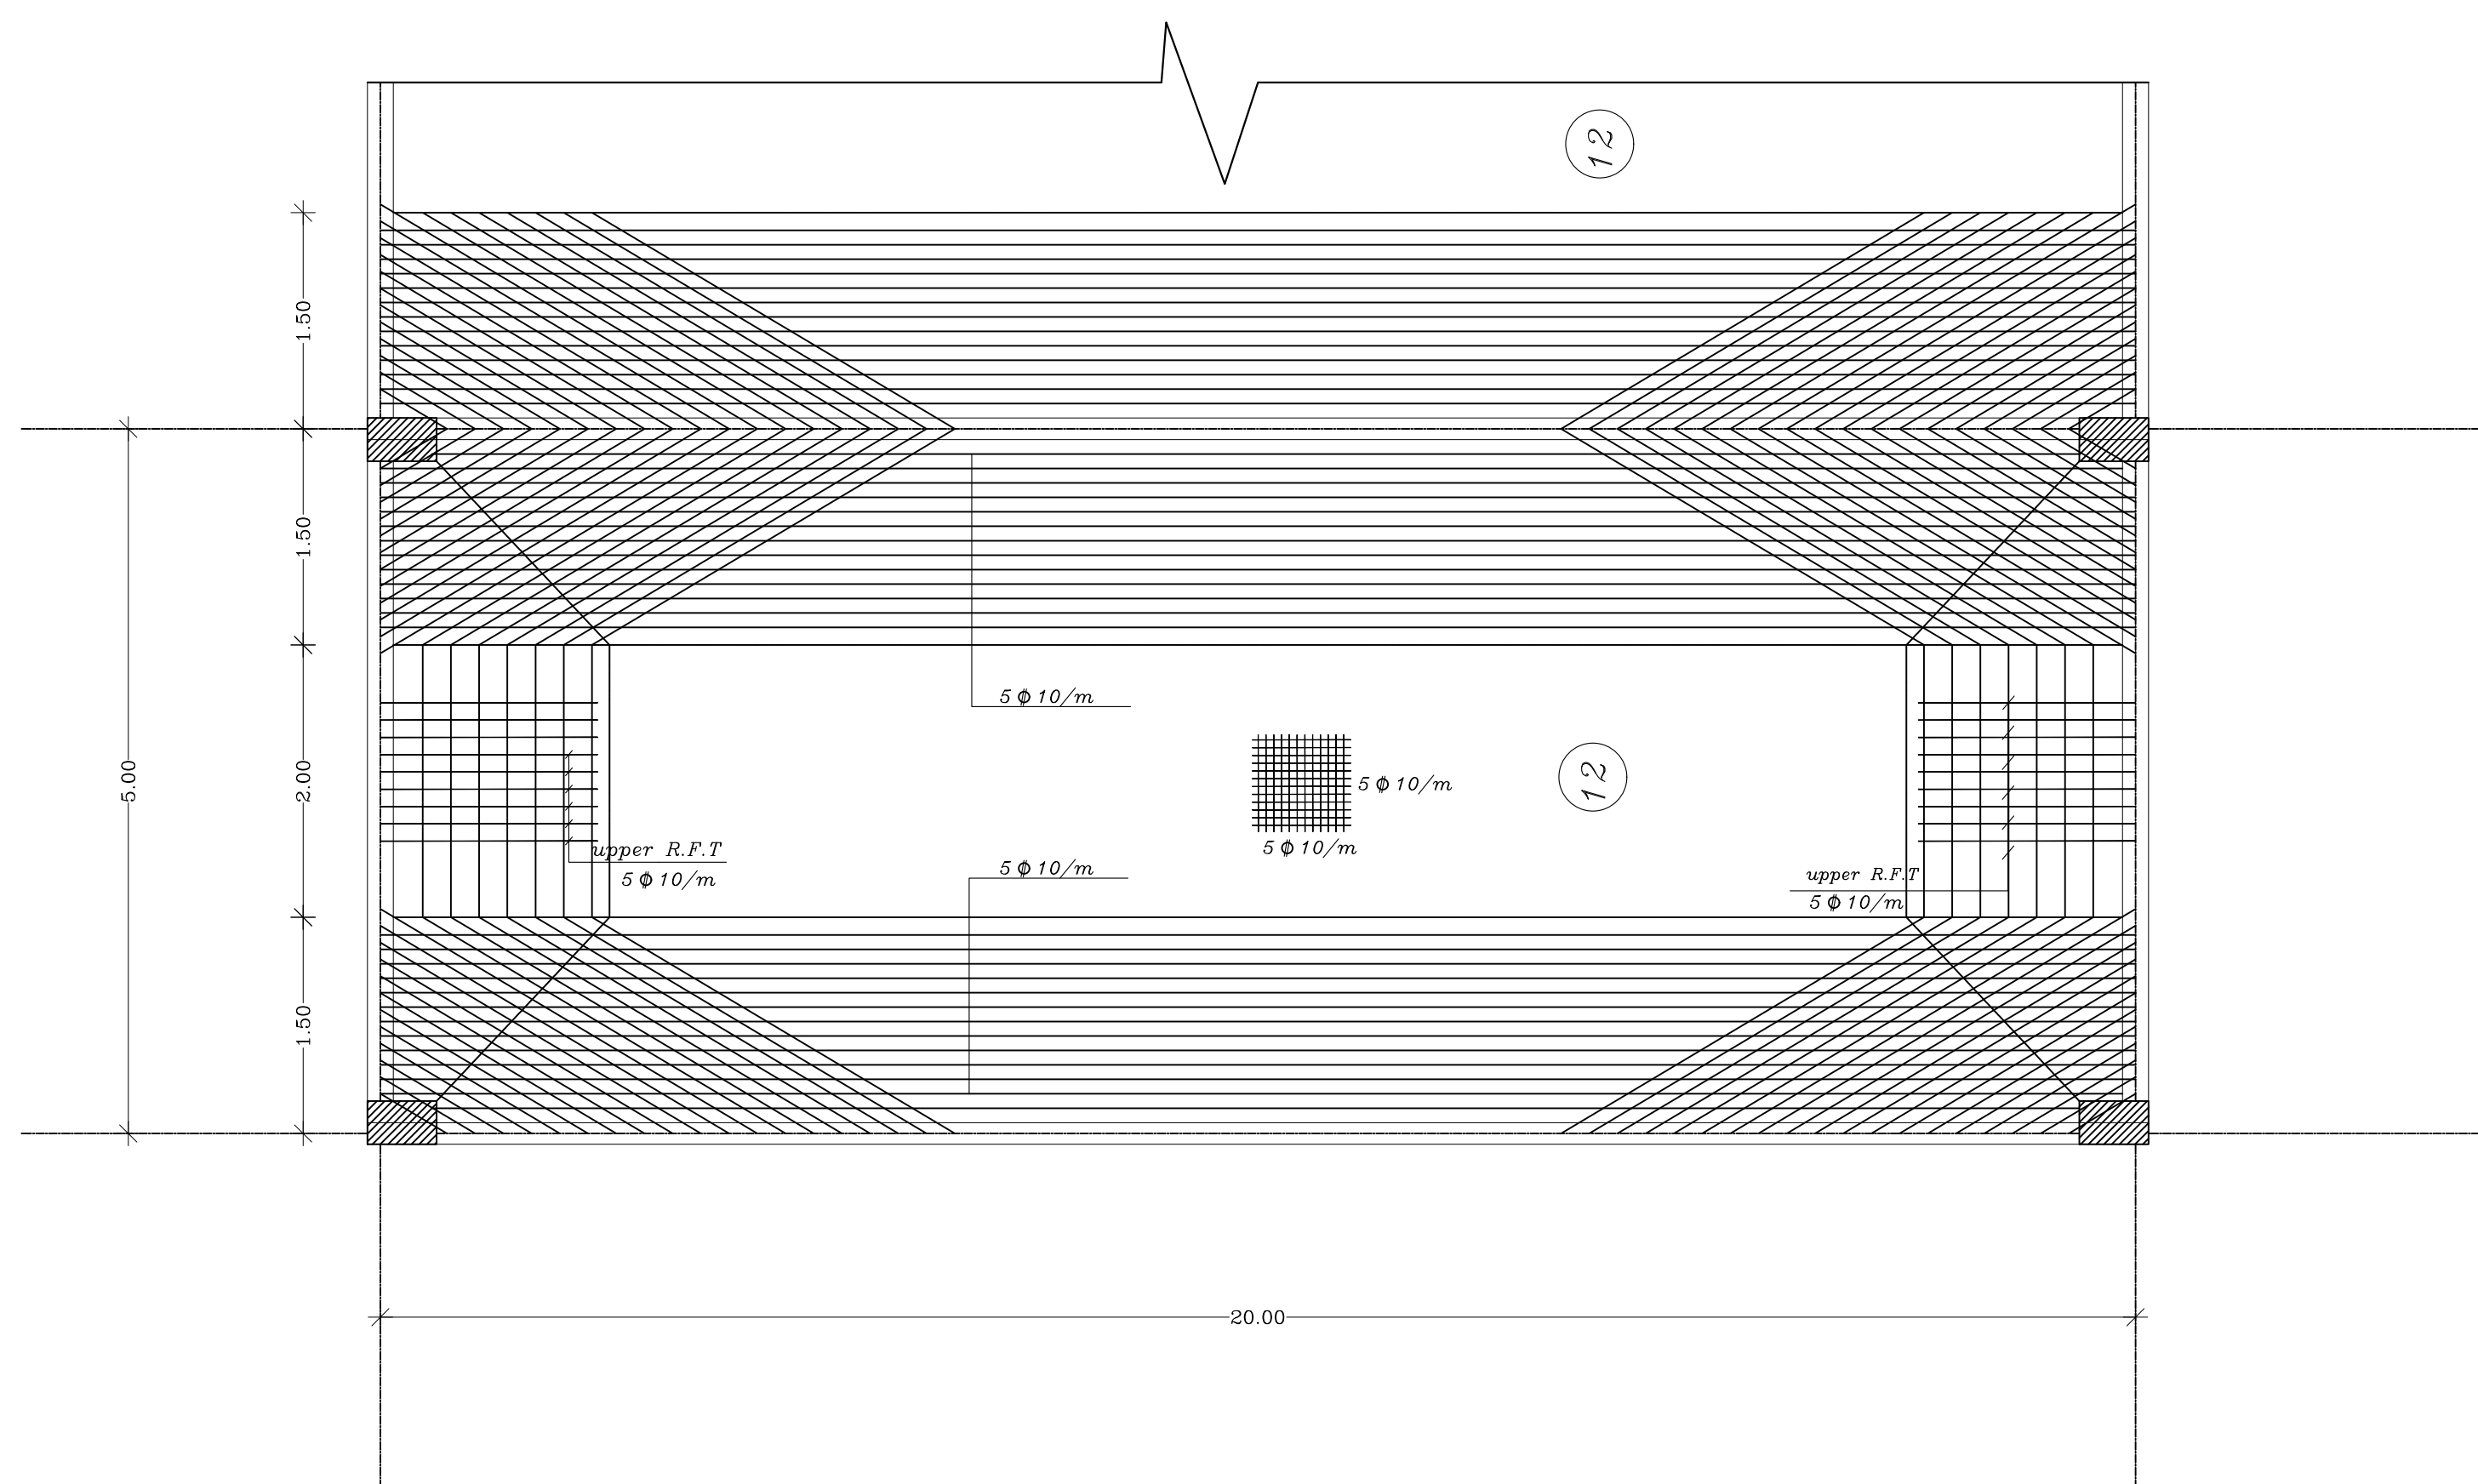

DETAILS OF RFT IN PLAN

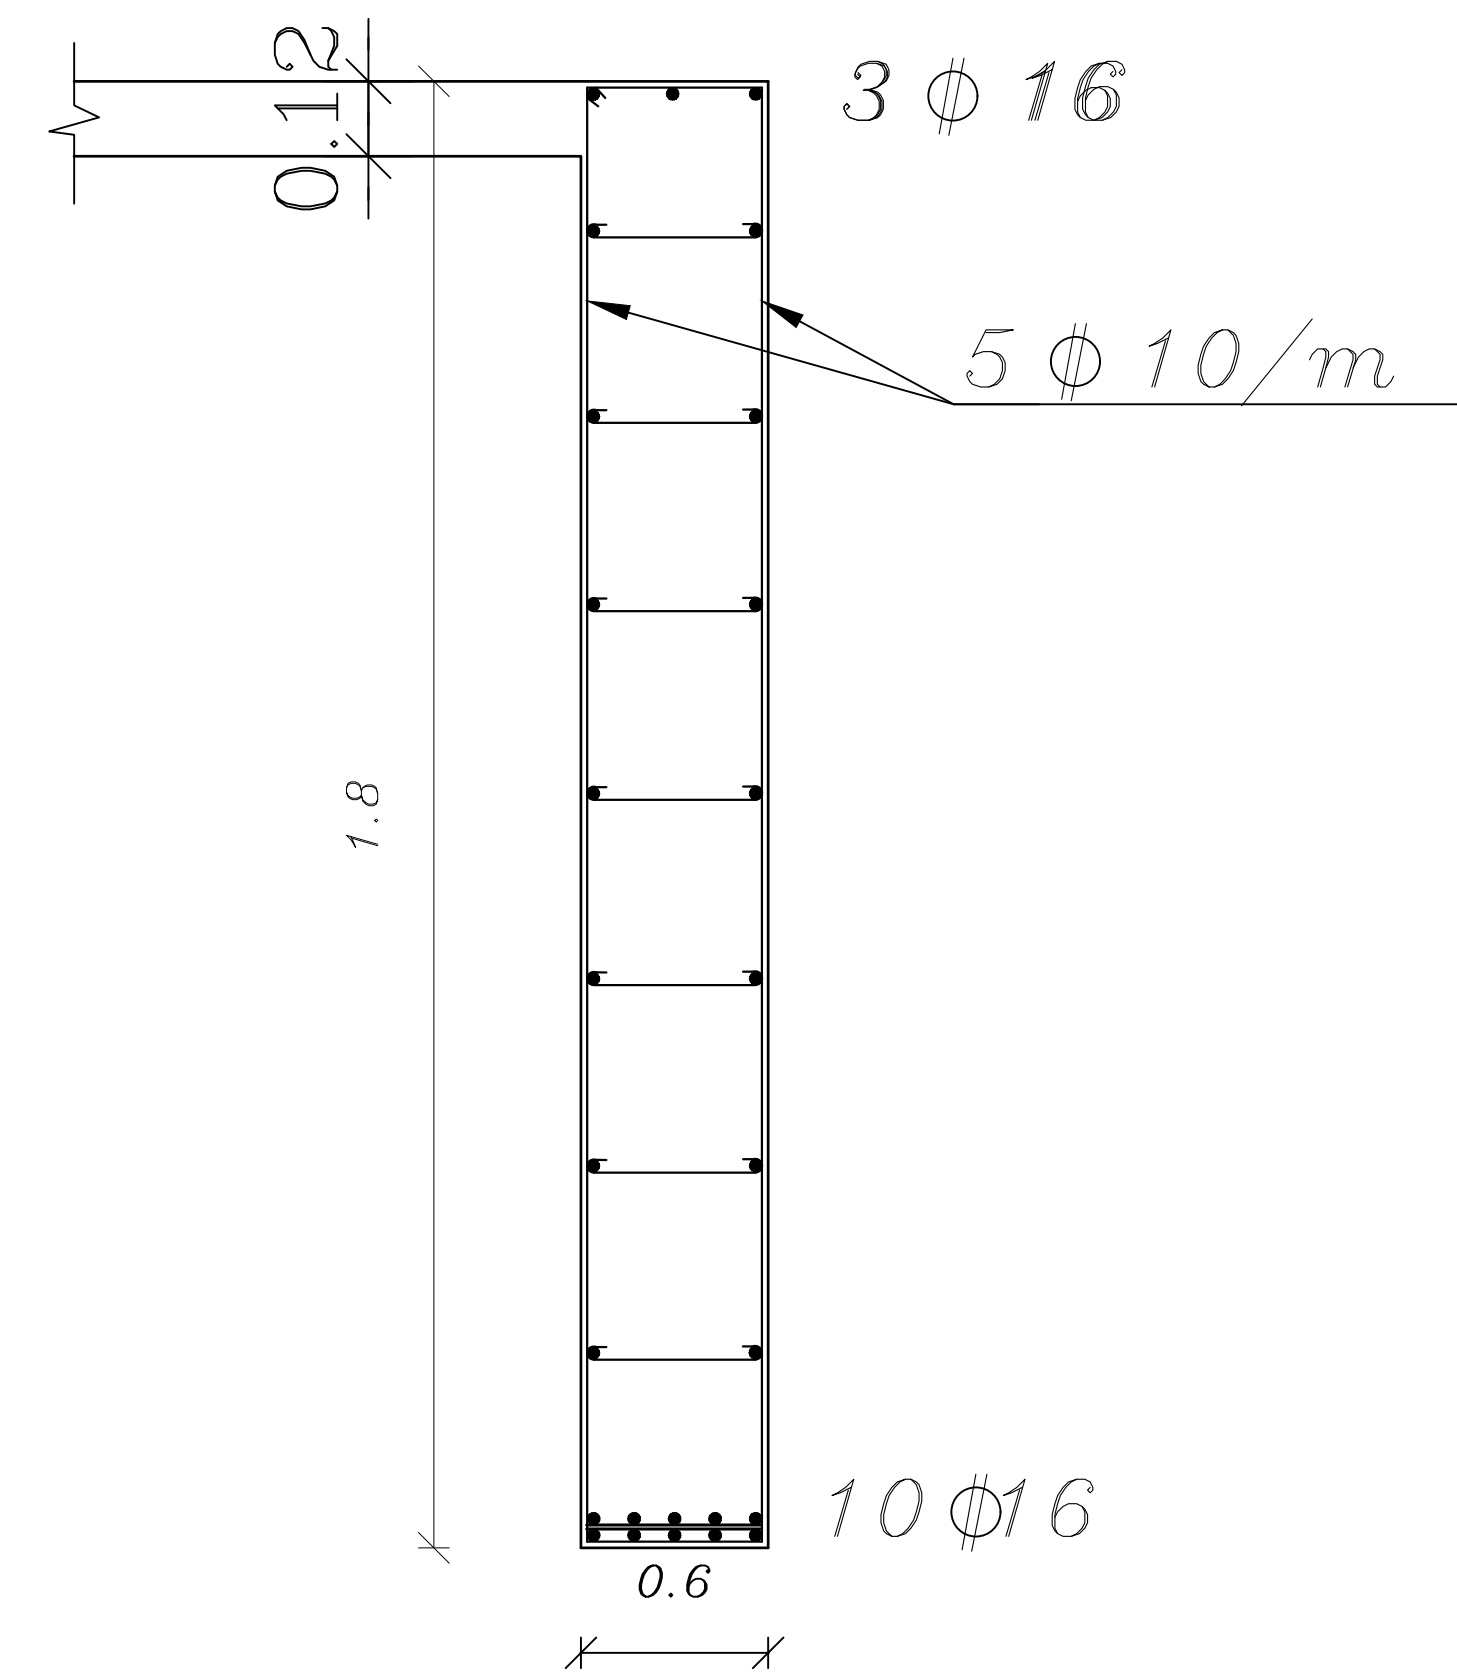

SEC (X-X)



Faculty of Engineering
Cairo University
Civil Department

NOTES :

- 1- ALL DIMENSIONS AND AXES SHOULD BE READ IN CONJUNCTION WITH ARCHITECTURAL DRAWINGS BEFORE CONSTRUCTION.
- 2 - ALL DIMENSION AND LEVELS ARE IN M UNLESS OTHERWISE NOTED ON PLAN.
- 3 - THE CUBIC STRENGTH OF R. CONCRETE USED IN ALL R.C. WORKS AFTER 28 DAYS SHOULD NOT BE LESS THAN 250 Kg/cm².
- 4 - THE CEMENT USED FOR BOTH PLAIN AND REINFORCED CONCRETE UNDER GROUND LEVEL IS SULPHATE RESISTENCE PORTLAND CEMENT.
- 5 - STEEL USED IN RFT. IN R.C. WORK IS HIGH TENSILE STEEL "36/54" FOR DIAMETERS 10 mm AND MILD STEEL "24/35" FOR 8mm.
- 6 - THE REINFORCEMENT OF COULMNS WILL BE TAKEN FROM COULMNS DETAILS.
- 7 - CONCRETE COVER SHOULD NOT LESS THAN 2.5 cm FOR COULMNS.

PROJECT NAME :


HALL UNIT

By :

Anas Akram Saeed

DRAWING TITLE :

Footings

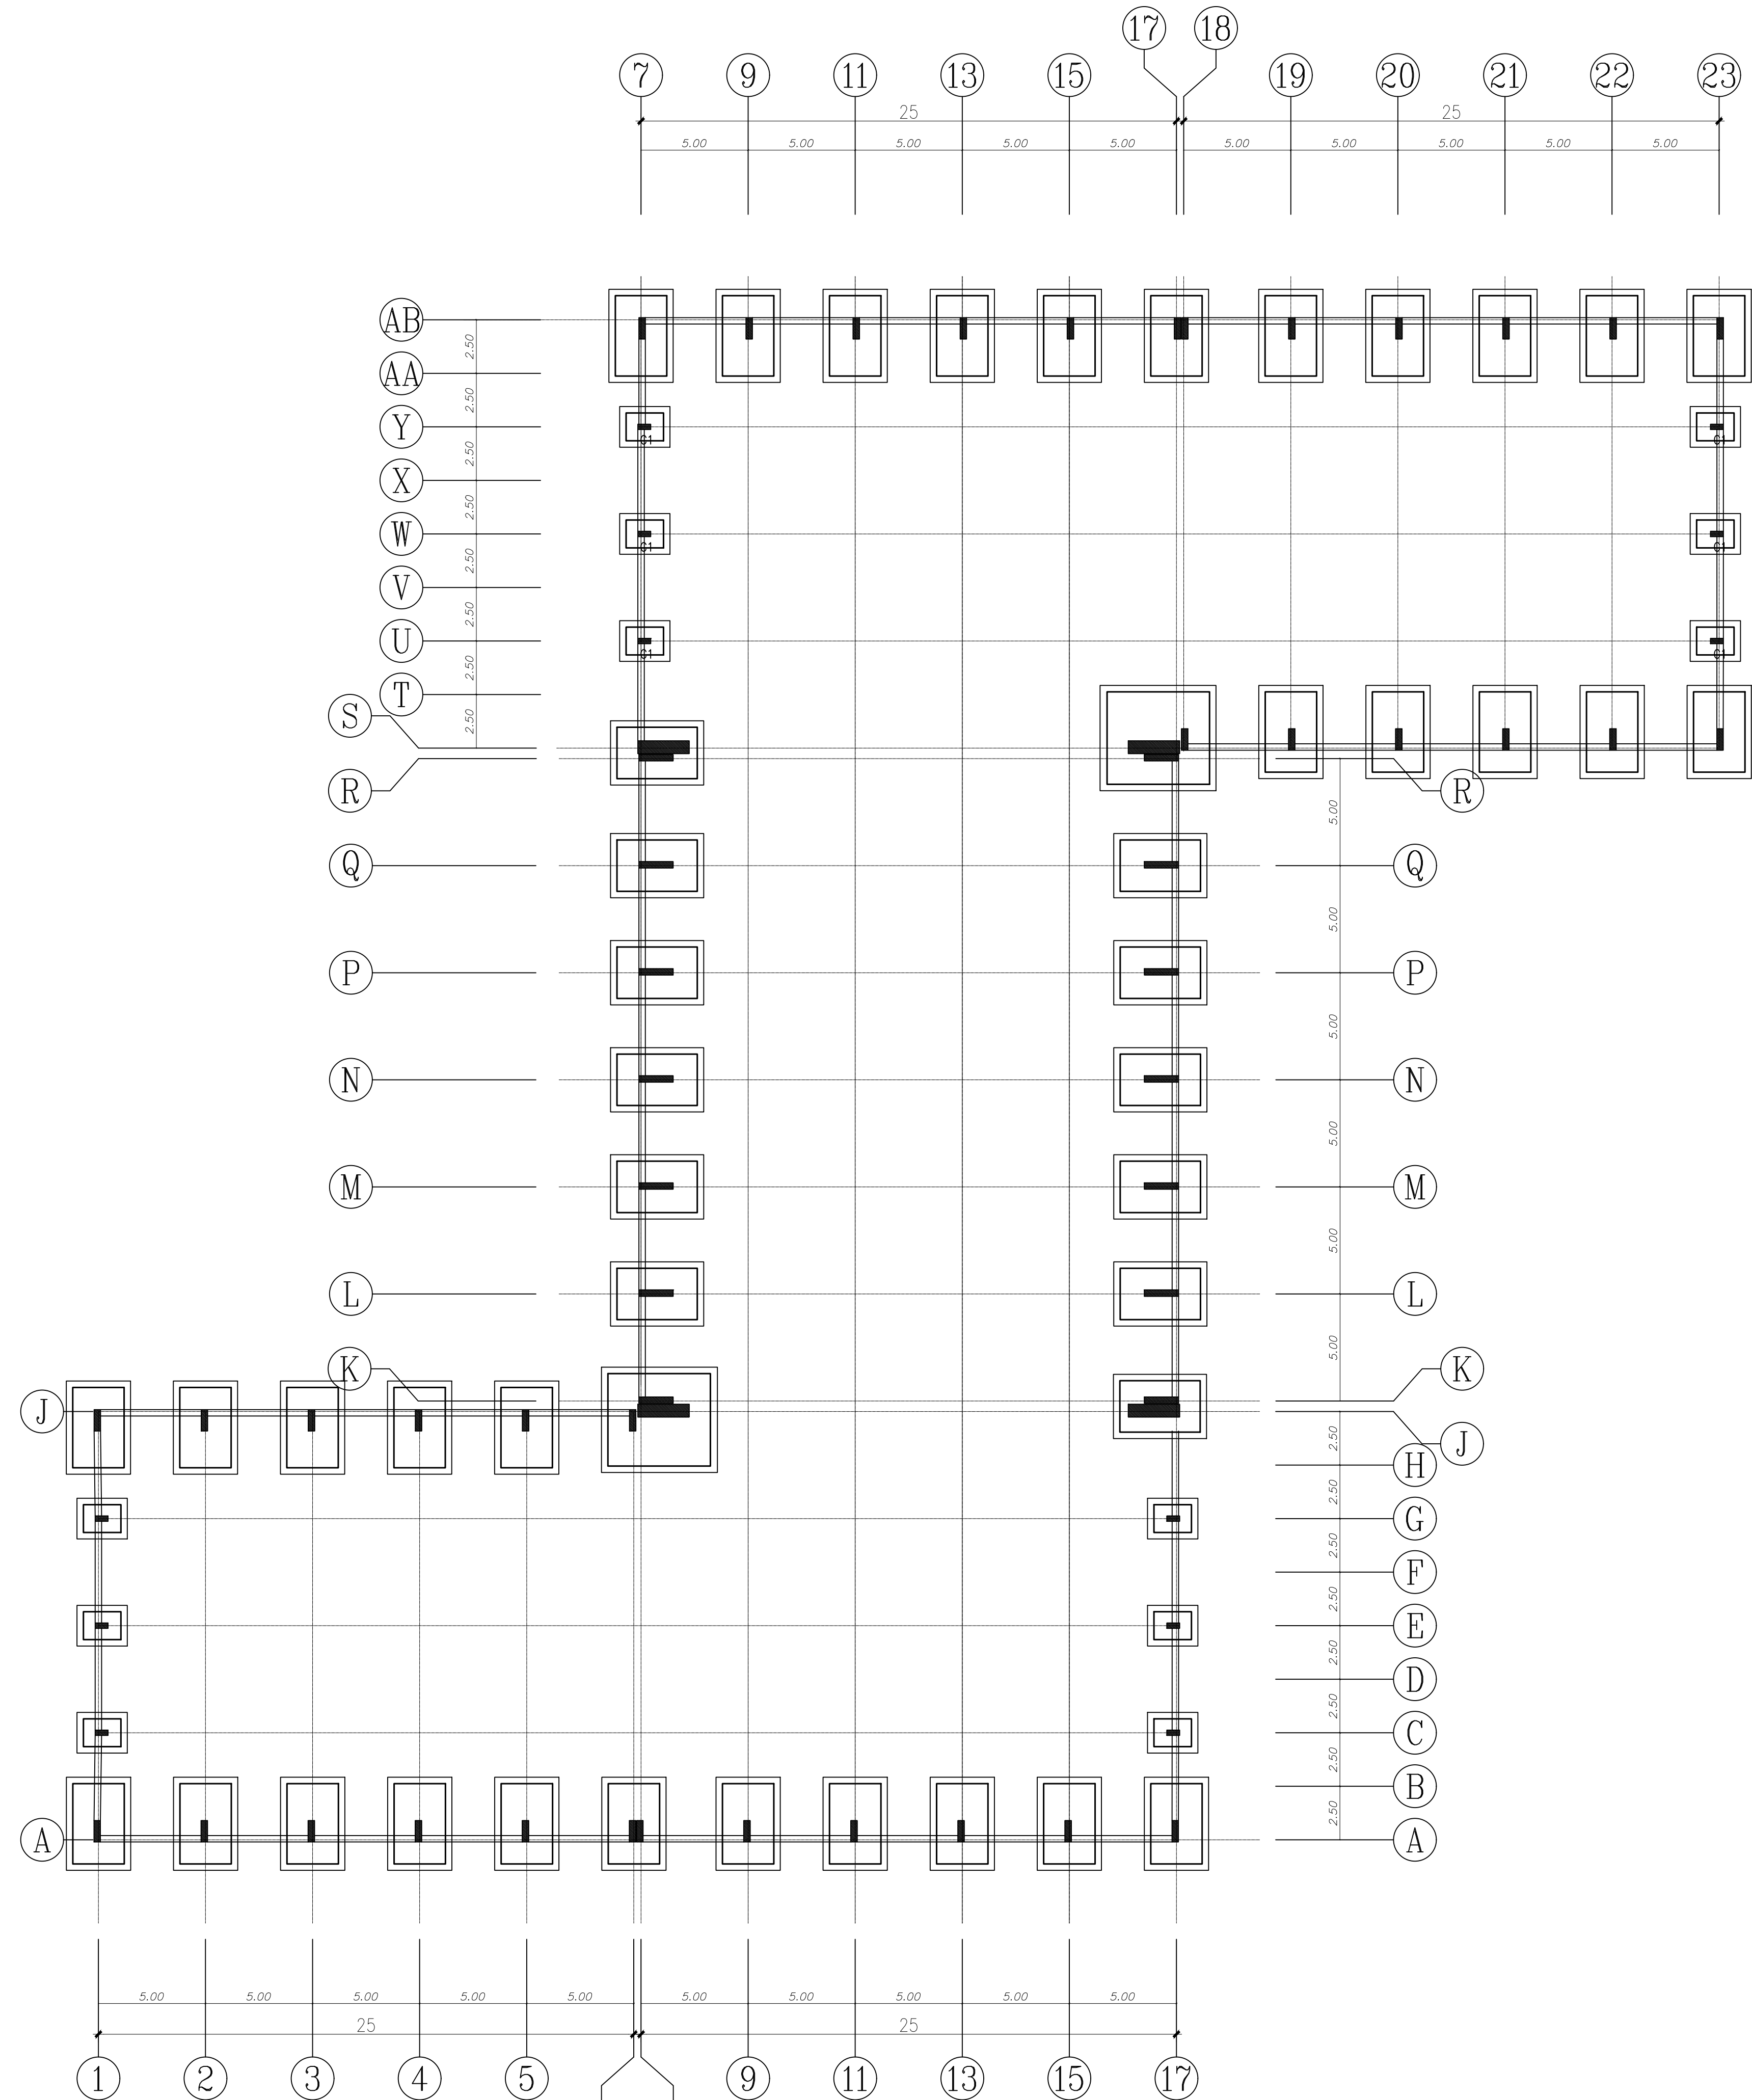



Faculty of Engineering
Cairo University
Civil Department

NOTES :

- 1- ALL DIMENSIONS AND AXES SHOULD BE READ IN CONJUNCTION WITH ARCHITECTURAL DRAWINGS BEFORE CONSTRUCTION.
- 2 - ALL DIMENSION AND LEVELS ARE IN M UNLESS OTHERWISE NOTED ON PLAN.
- 3 - THE CUBIC STRENGTH OF R. CONCRETE USED IN ALL R.C. WORKS AFTER 28 DAYS SHOULD NOT BE LESS THAN 250 Kg/cm².
- 4 - THE CEMENT USED FOR BOTH PLAIN AND REINFORCED CONCRETE UNDER GROUND LEVEL IS SULPHATE RESISTENCE PORTLAND CEMENT.
- 5 - STEEL USED IN RFT. IN R.C. WORK IS HIGH TENSILE STEEL "36/54" FOR DIAMETERS 10 mm AND MILD STEEL "24/35" FOR 8mm.
- 6 - THE REINFORCMENT OF COULMNS WILL BE TAKEN FROM COULMNS DETAILS.
- 7 - CONCRETE COVER SHOULD NOT LESS THAN 2.5 cm FOR COULMNS.

PROJECT NAME :


HALL UNIT

By :

Anas Akram Saeed

DRAWING TITLE :

Double curved Shell RFT

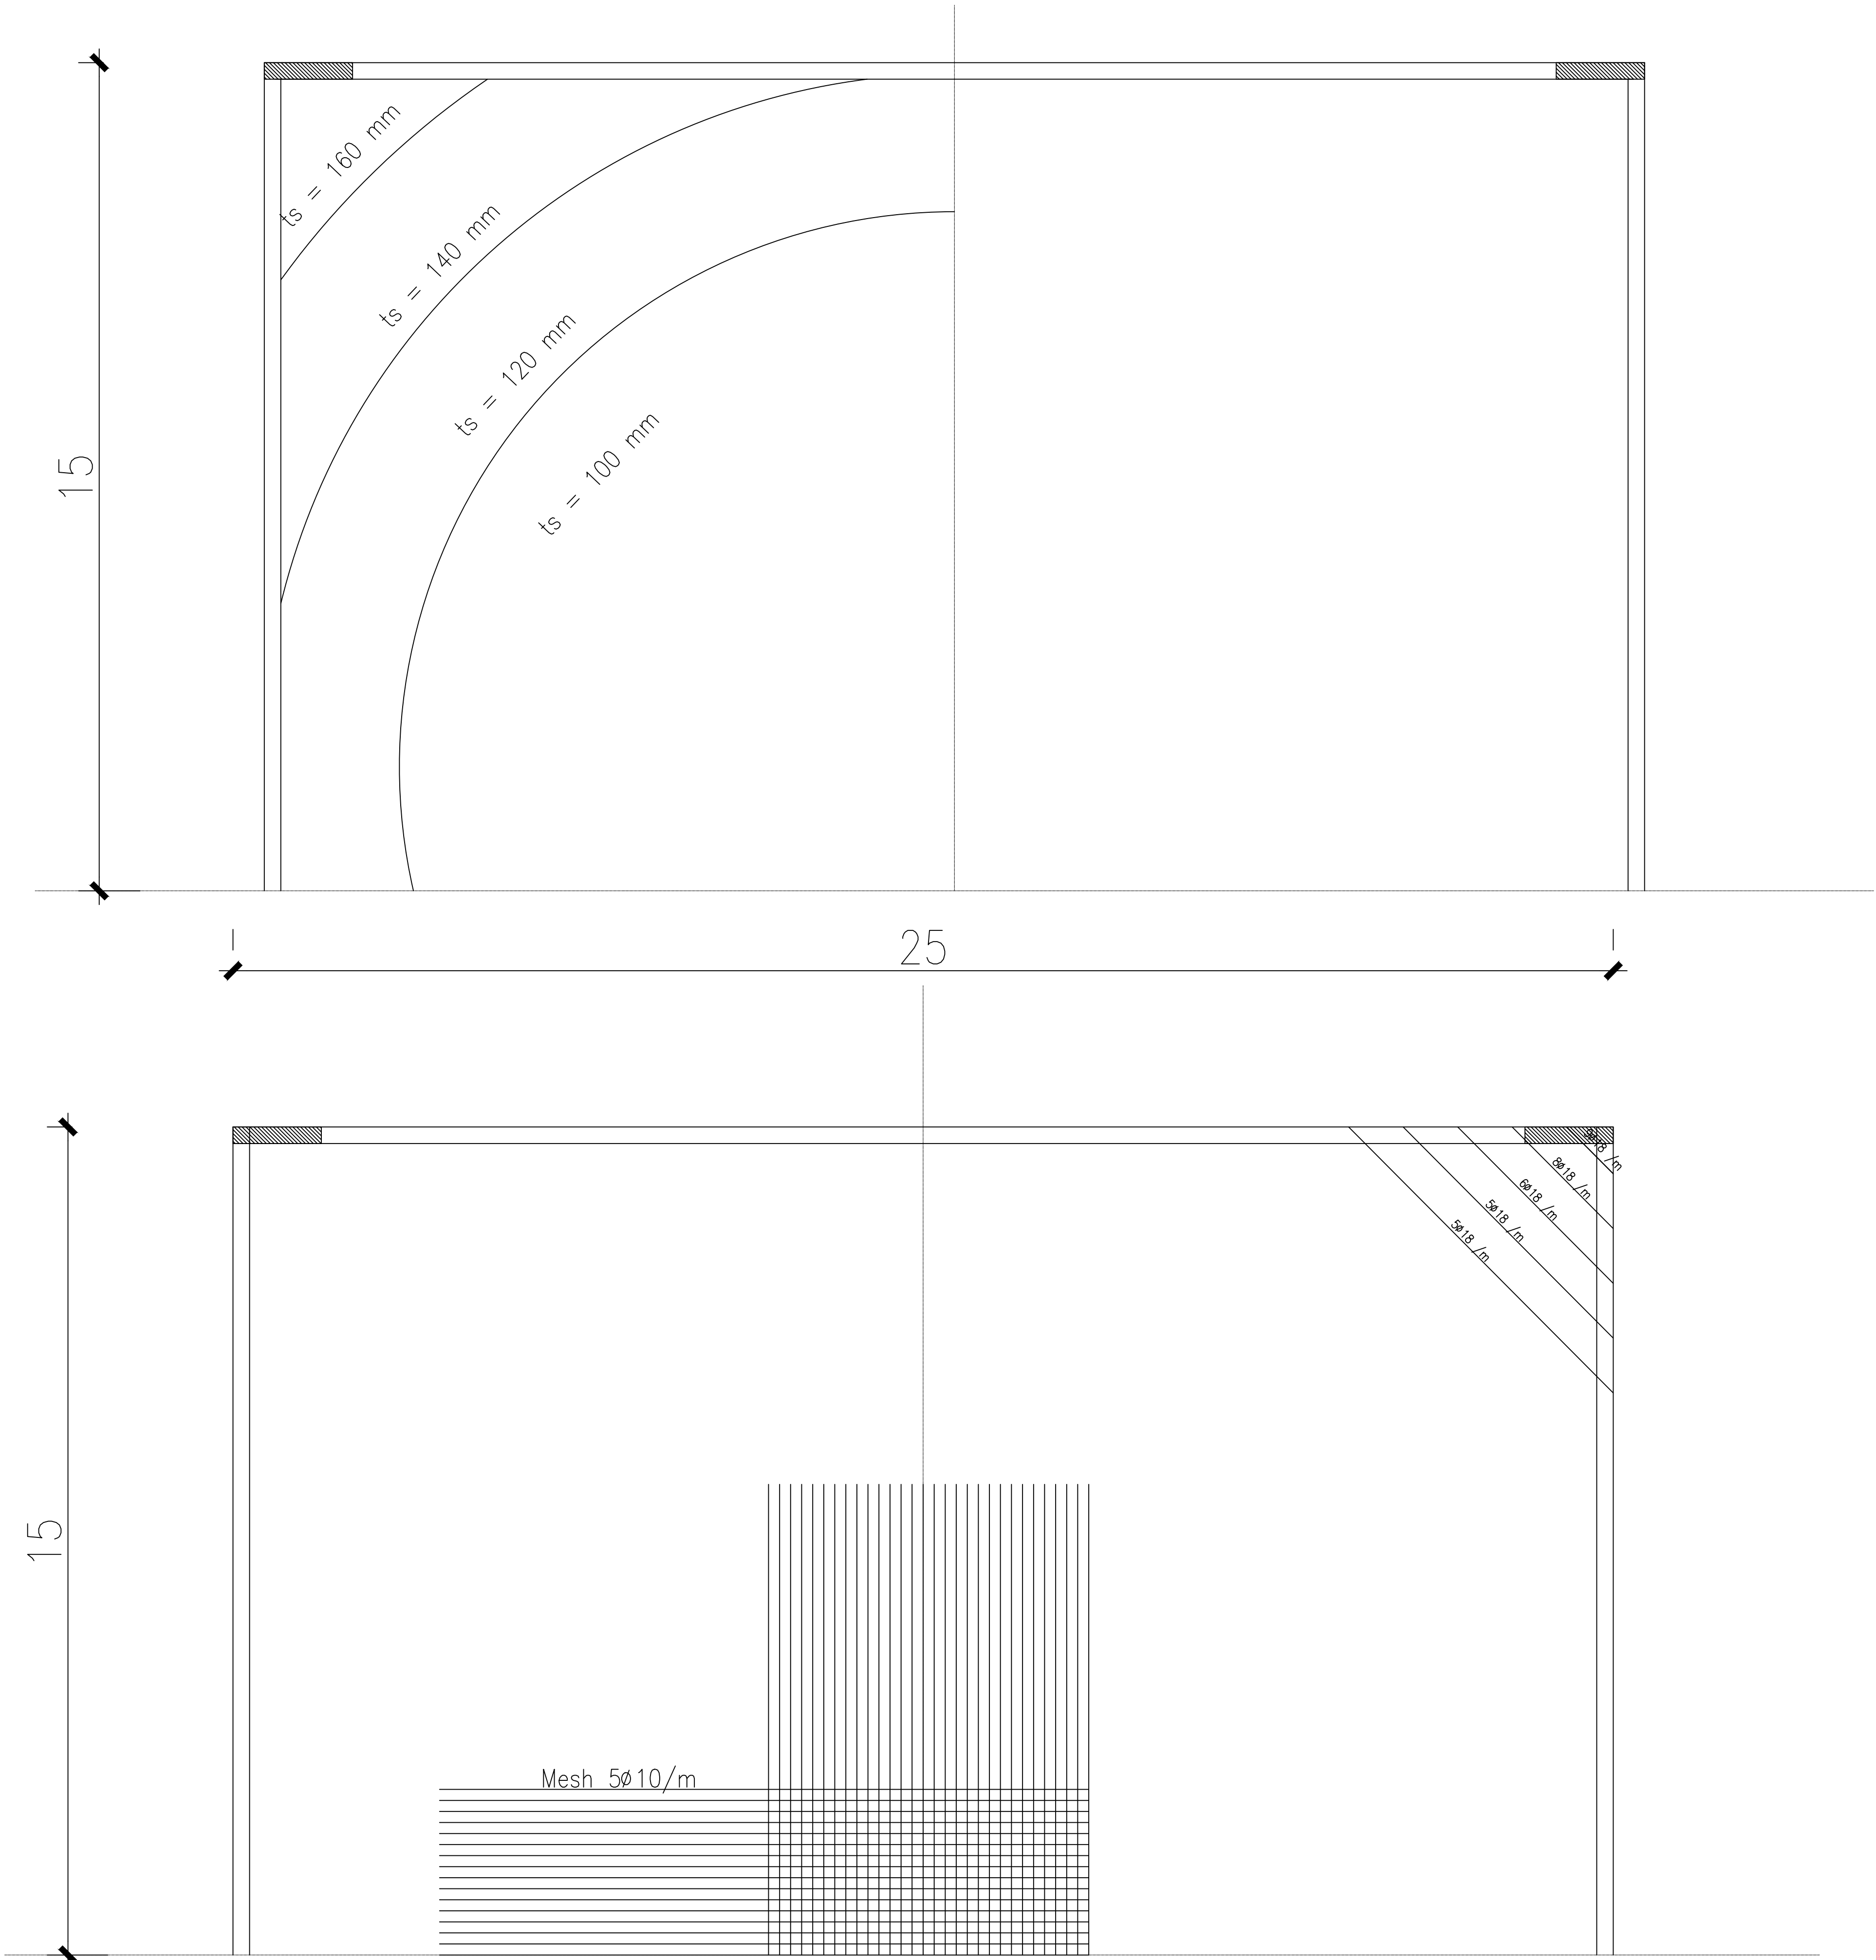



Faculty of Engineering
Cairo University
Civil Department

NOTES :

- 1- ALL DIMENSIONS AND AXES SHOULD BE READ IN CONJUNCTION WITH ARCHITECTURAL DRAWINGS BEFORE CONSTRUCTION.
- 2 - ALL DIMENSION AND LEVELS ARE IN M UNLESS OTHERWISE NOTED ON PLAN.
- 3 - THE CUBIC STRENGTH OF R. CONCRETE USED IN ALL R.C. WORKS AFTER 28 DAYS SHOULD NOT BE LESS THAN 250 Kg/cm² .
- 4 - THE CEMENT USED FOR BOTH PLAIN AND REINFORCED CONCRETE UNDER GROUND LEVEL IS SULPHATE RESISTENCE PORTLAND CEMENT.
- 5 - STEEL USED IN RFT. IN R.C. WORK IS HIGH TENSILE STEEL "36/54" FOR DIAMETERS 10 mm AND MILD STEEL "24/35" FOR 8mm.
- 6 - THE REINFORCEMENT OF COULMNS WILL BE TAKEN FROM COULMNS DETAILS.
- 7 - CONCRETE COVER SHOULD NOT LESS THAN 2.5 cm FOR COULMNS.

PROJECT NAME :

HALL UNIT

By :

Anas Akram Saeed

DRAWING TITLE :

Axis and Columns

